

ARCHITECTURAL PORTFOLIO

SNEHA HOLE

DR. D. Y. PATIL COLLEGE OF ARCHITECTURE, AKURDI

CURRICULUM VITAE



ABOUT ME
A great building must begin with the immeasurable, must go through measurable means when it is being designed, and in the end must be unmeasured.
- Louis Kahn

SNEHA BALASAHEB HOLE
A R C H I T E C T

CONTACT
8308882563 9834371392
Snehal Society, Flat No-3, Plot no-RH/18g, Block No-G, MIDC, Chikhali Road, Near Kasturi Market Sambhajinagar, Chinchwad, Pune Maharashtra-411019
snehahole3696@gmail.com

Additionally I achieved A Grade in Elementary and Intermediate competitive exams which is based on sketching and painting Even in sports I have collected certificates on District and State Level.

WORK
I have done my Internship in Pimpri at DREAM SPACE ARCHITECTS which owns AR. MAHENDRA THAKUR
Bungalow design of mahendra thakur at chinchwad pune
Commercial with Bungalow design of client Mr. Hanumant Jadhav sir at Chikhali,Pune
Industrial Measurement drawing of Syska Pvt.Lmt Industry at Chakan of the owner Mr. Sahebrao Patil of Sahebra Foundation
Stage decorations, model making, college fest decorations, NASA, buildtech on the college level

PERSONAL
3 June 1996 Unmarried
English, Hindi, Marathi Indian

HOBBIES
Sketching and Painting Photography
Reading Travelling
Swimming Movies

INTEREST
Residential Projects, Commercial Projects, Interior Design Landscape Design

SOFTWARES SKILL
A 80% F 75% LUMINA 70% Ps 75% AutoCAD 50% WPS 75%

TABLE OF CONTENT

1. BUNGALOW	1
2. BUNGALOW	5
3. HOUSING	11
4. BUSINESS HUB	15
5. PERSONAL	18
6. THESIS : ECO-RESORT	19
7. LANDSCAPE DESIGN	29
8. WORKING DRAWING	31



BUNGALOW FOR FOREST OFFICER

GROUND FLOOR PLAN

FIRST FLOOR PLAN

**LOCATION : Talegaon Dabhade, Pune
SITE AREA : 980.45 SQM
BUILT UP AREA : 250 SQM**

The bungalow is designed for forest officer. The landscape of the bungalow is specially designed in such way that, that person can use this in his daily life.






Bungalow has landscape in such way that user can use it in daily life. Bungalow is surrounded by the jogging track so he can have walk in the morning. Landscape of bungalow have

parking
swimming pool yoga platform
outdoor gazebo Many species of
trees
vegetable garden





BUNGALOW

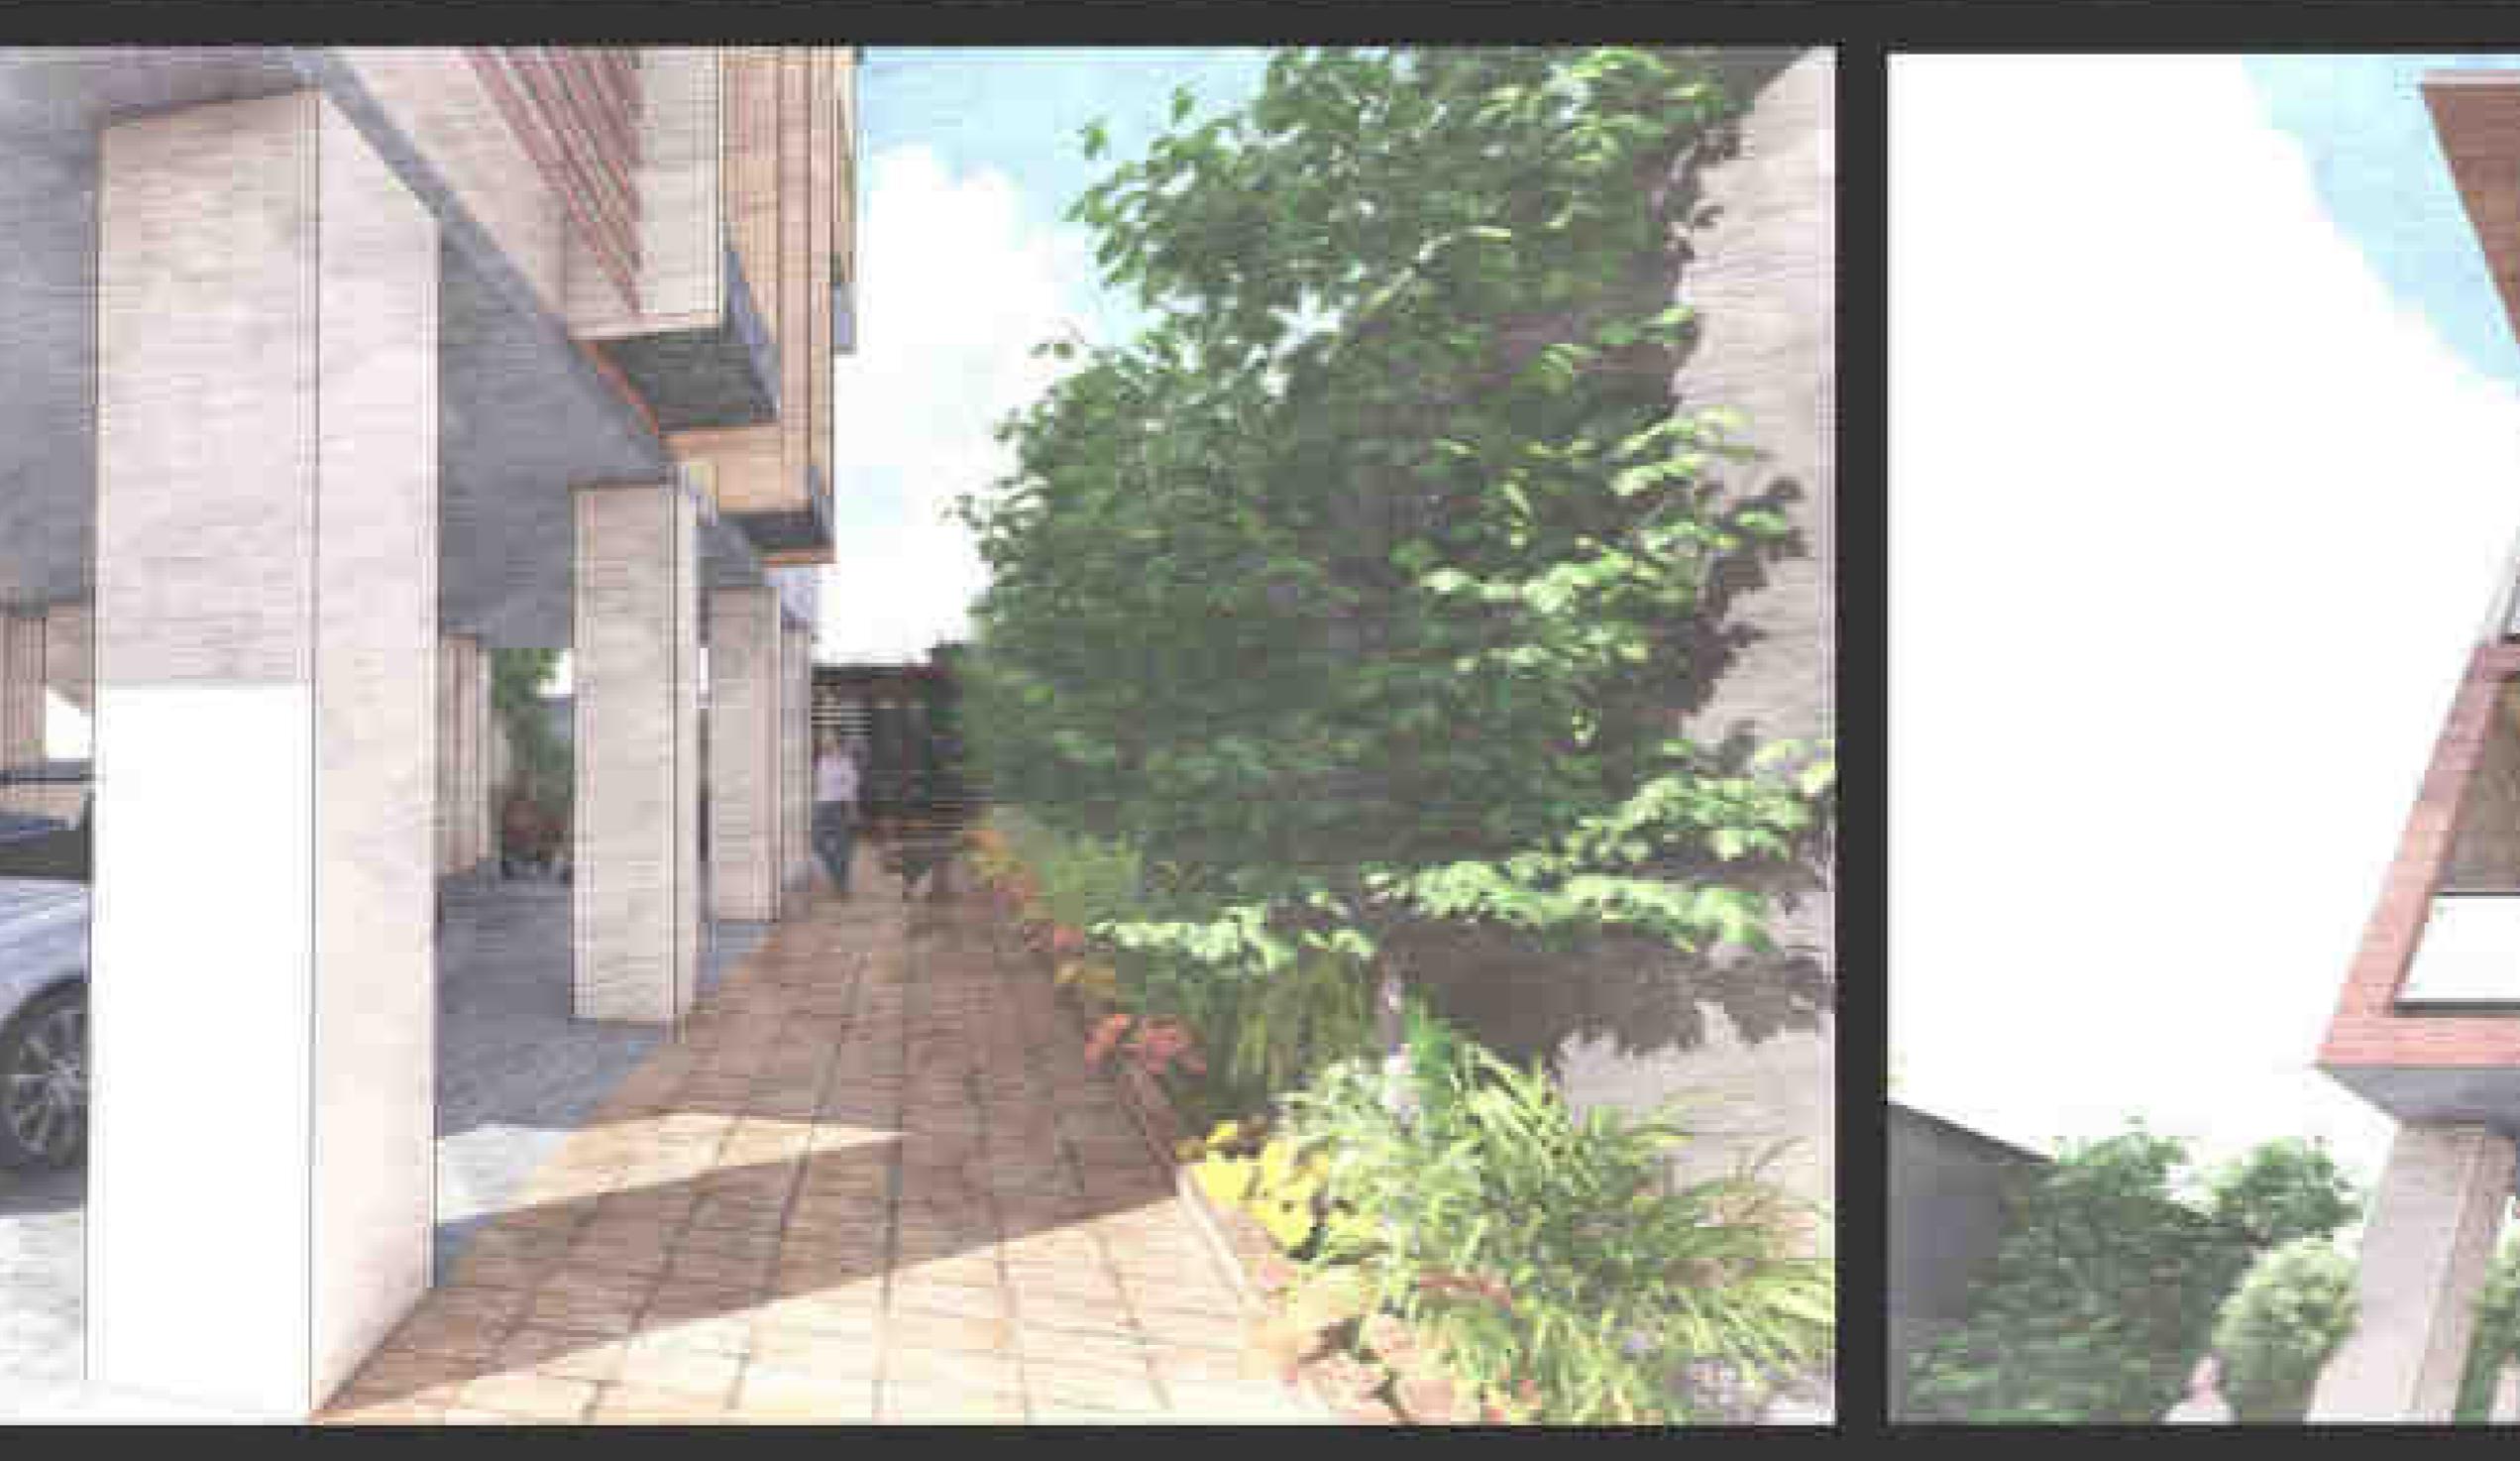






LUXURY HOUSING



Housing is the modern concept includes not only the 'Physical Structure' for providing protection and shelter but also includes the immediate surrounding and related community services and facilities. Housing is constructed for family life where a person gets physical and mental peace. World Health Organization [WHO] refers the term "Residential Environment" where family can develop and flourish physically, mentally and socially and it includes all necessary services, facilities and equipment and devices needed for physical and mental health and social well-being. It helps in promoting social relationships and community development




SITE PLAN

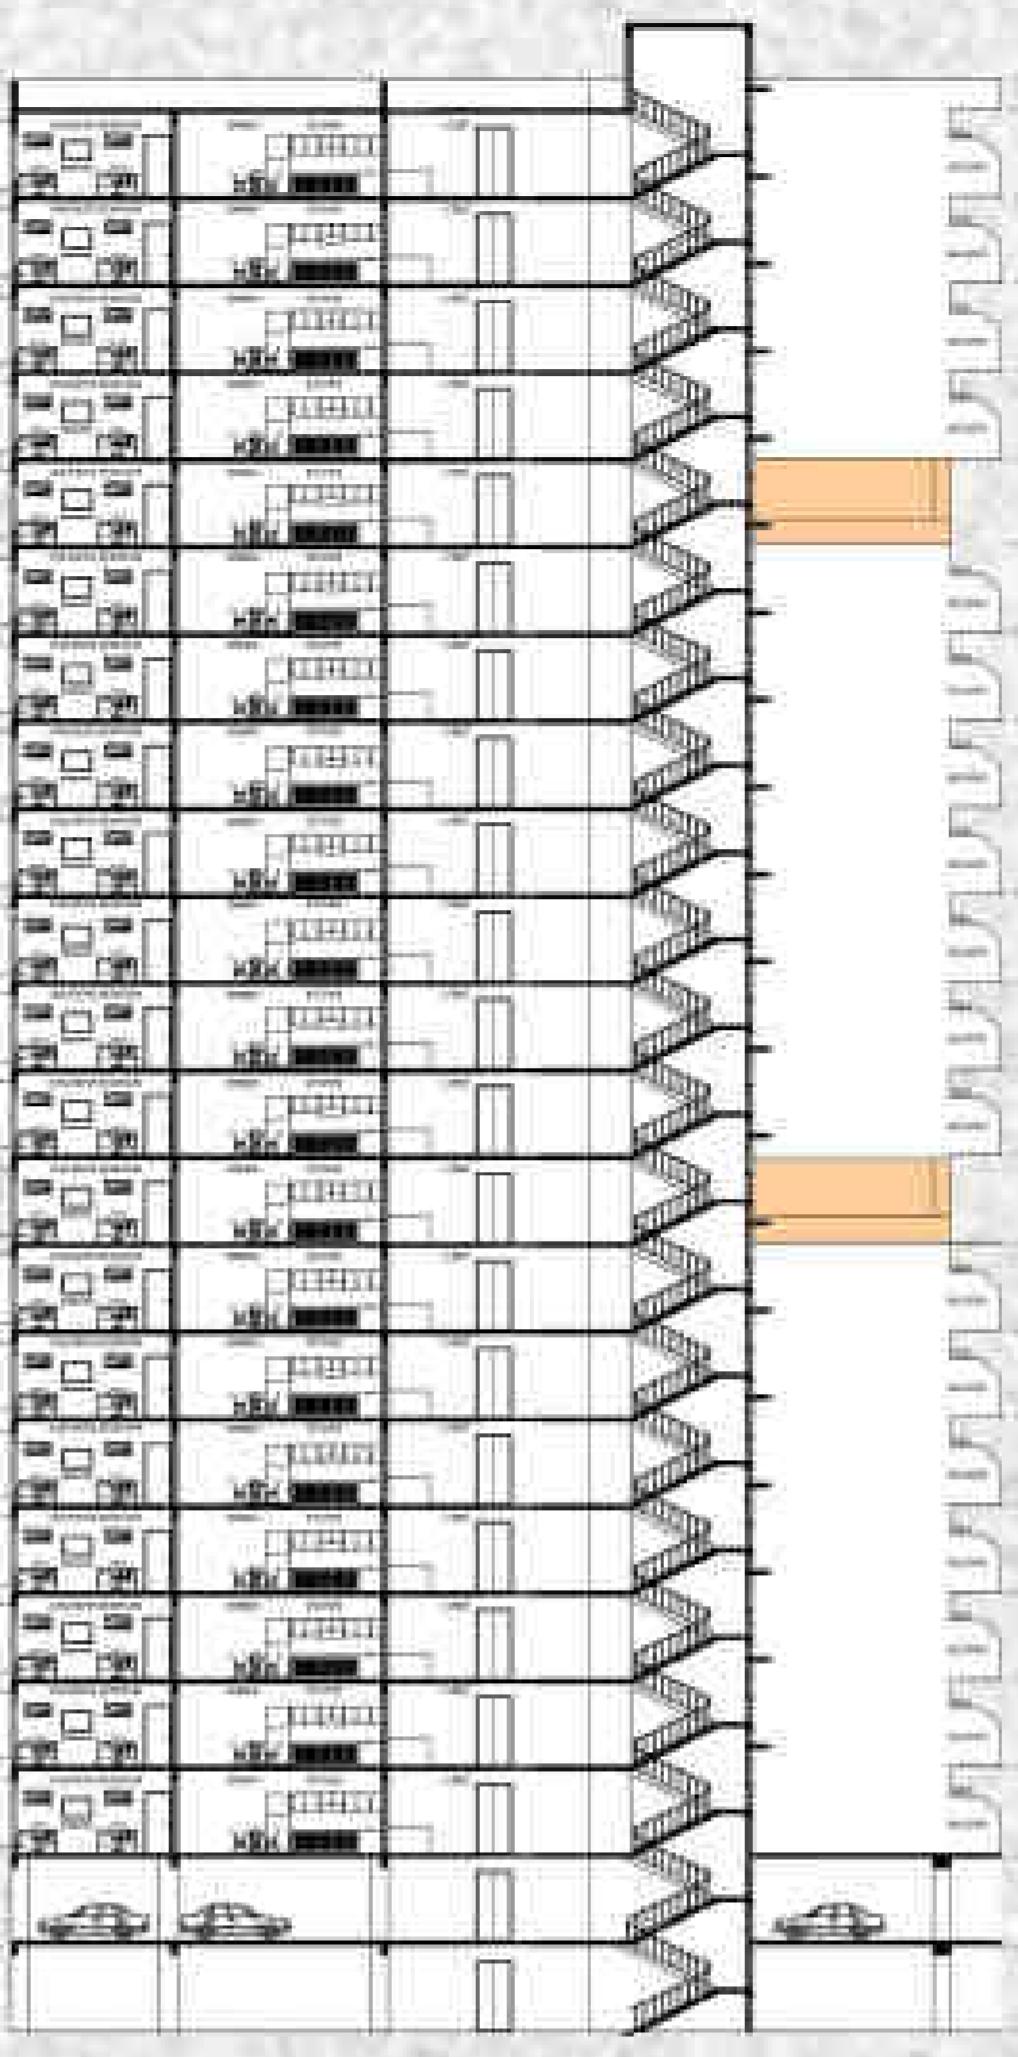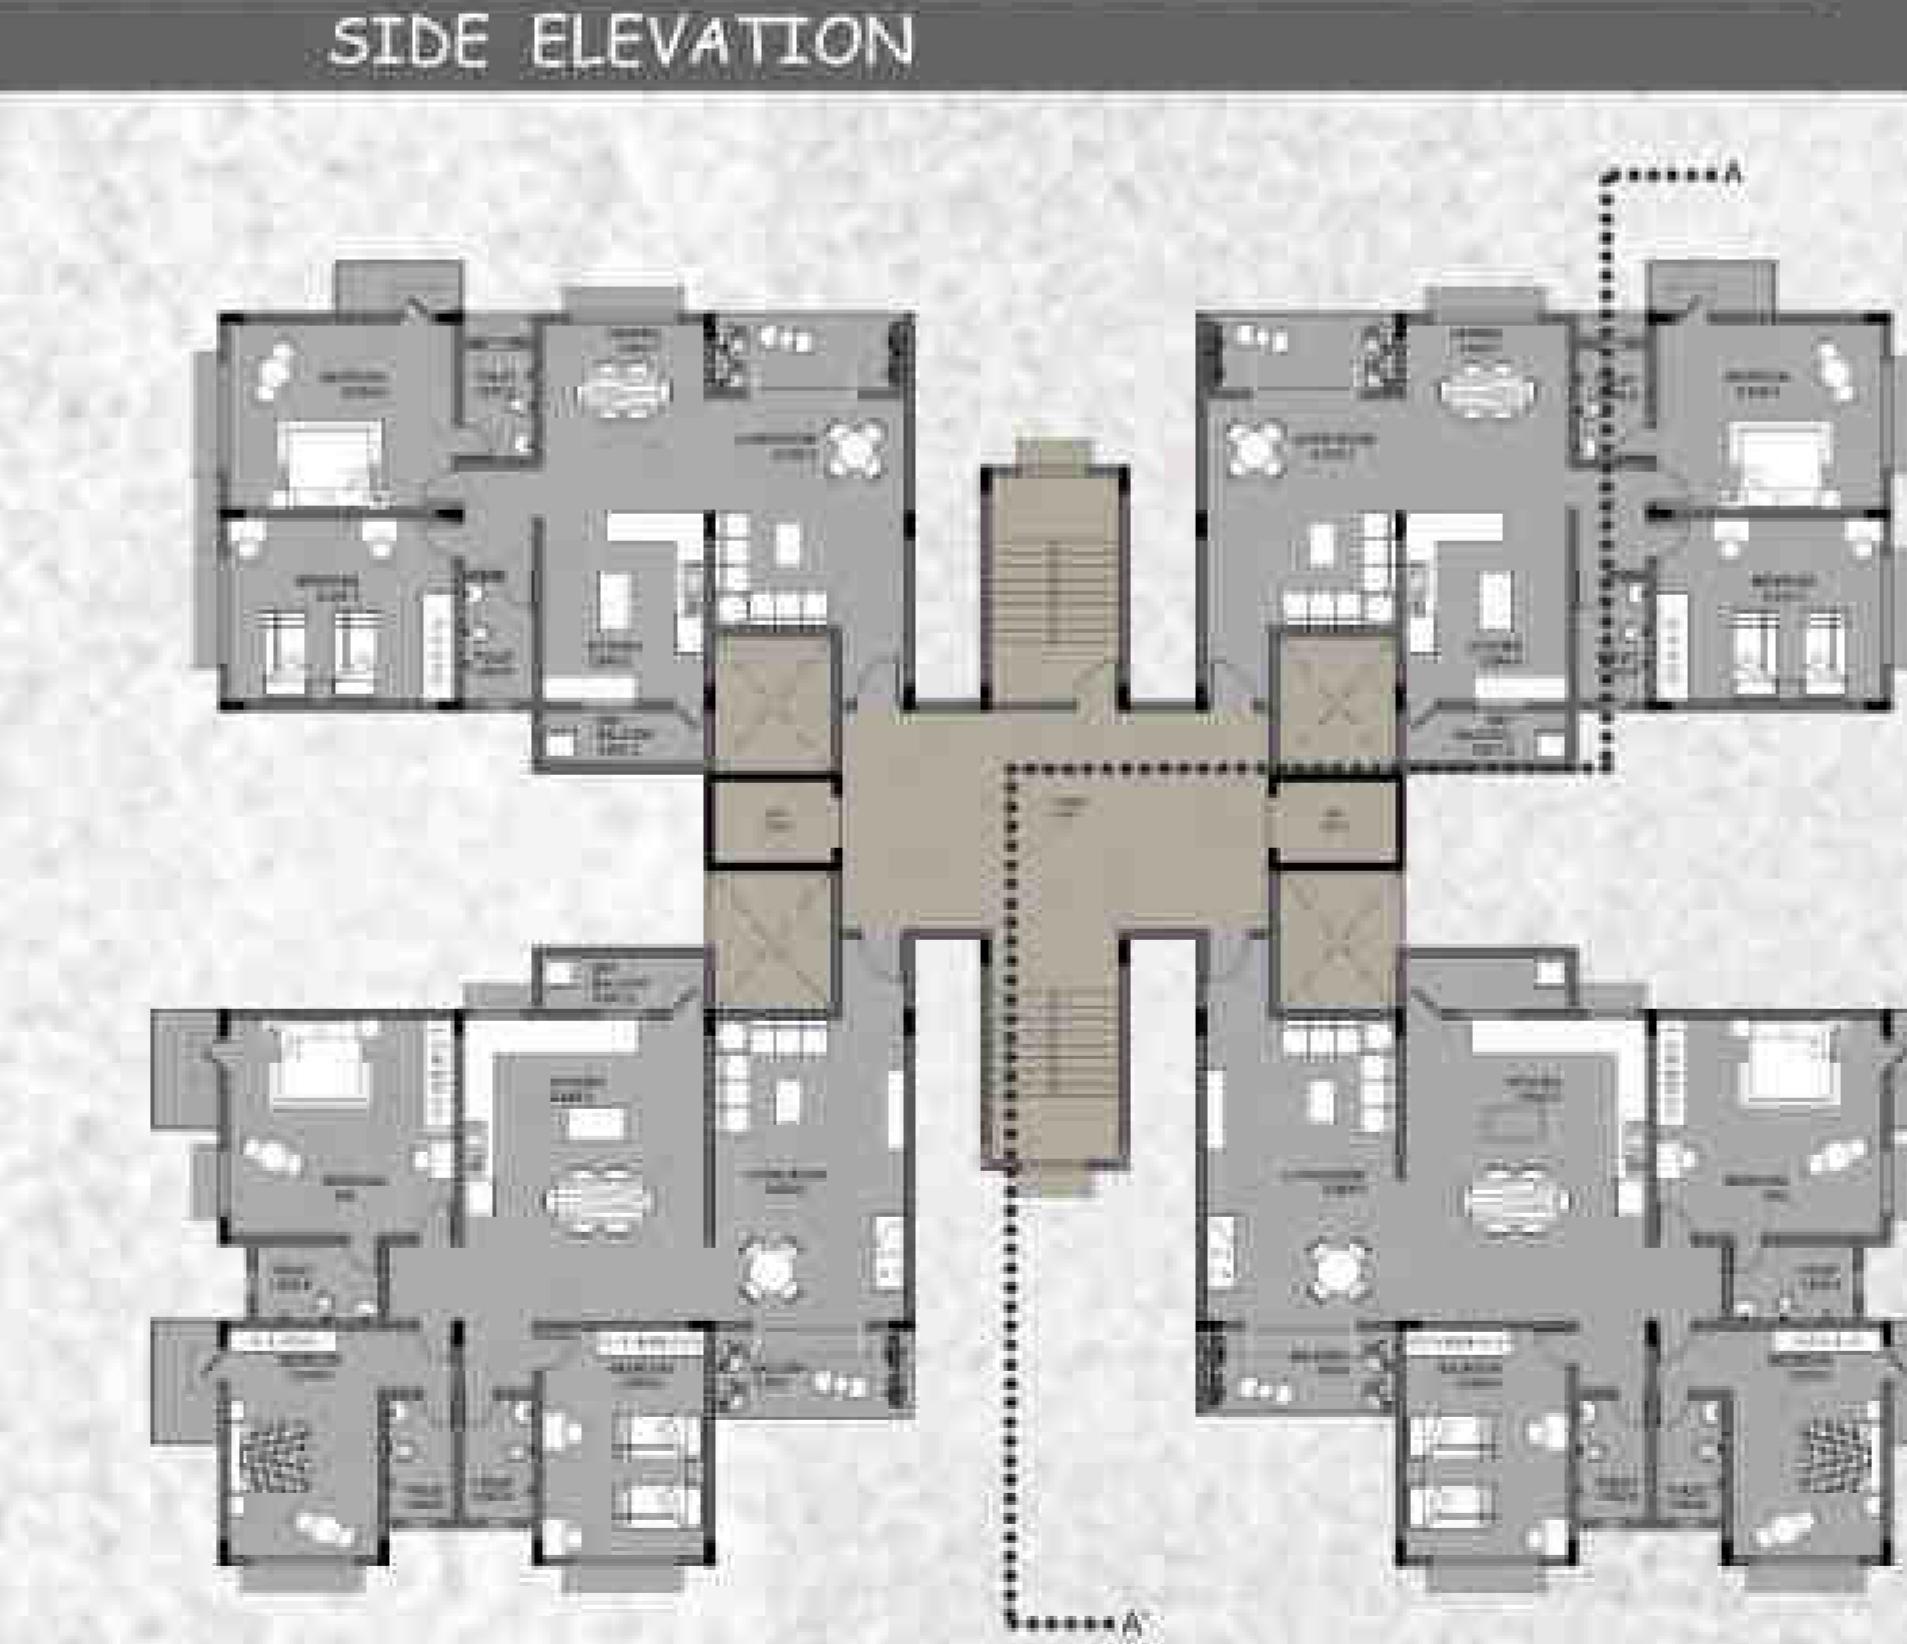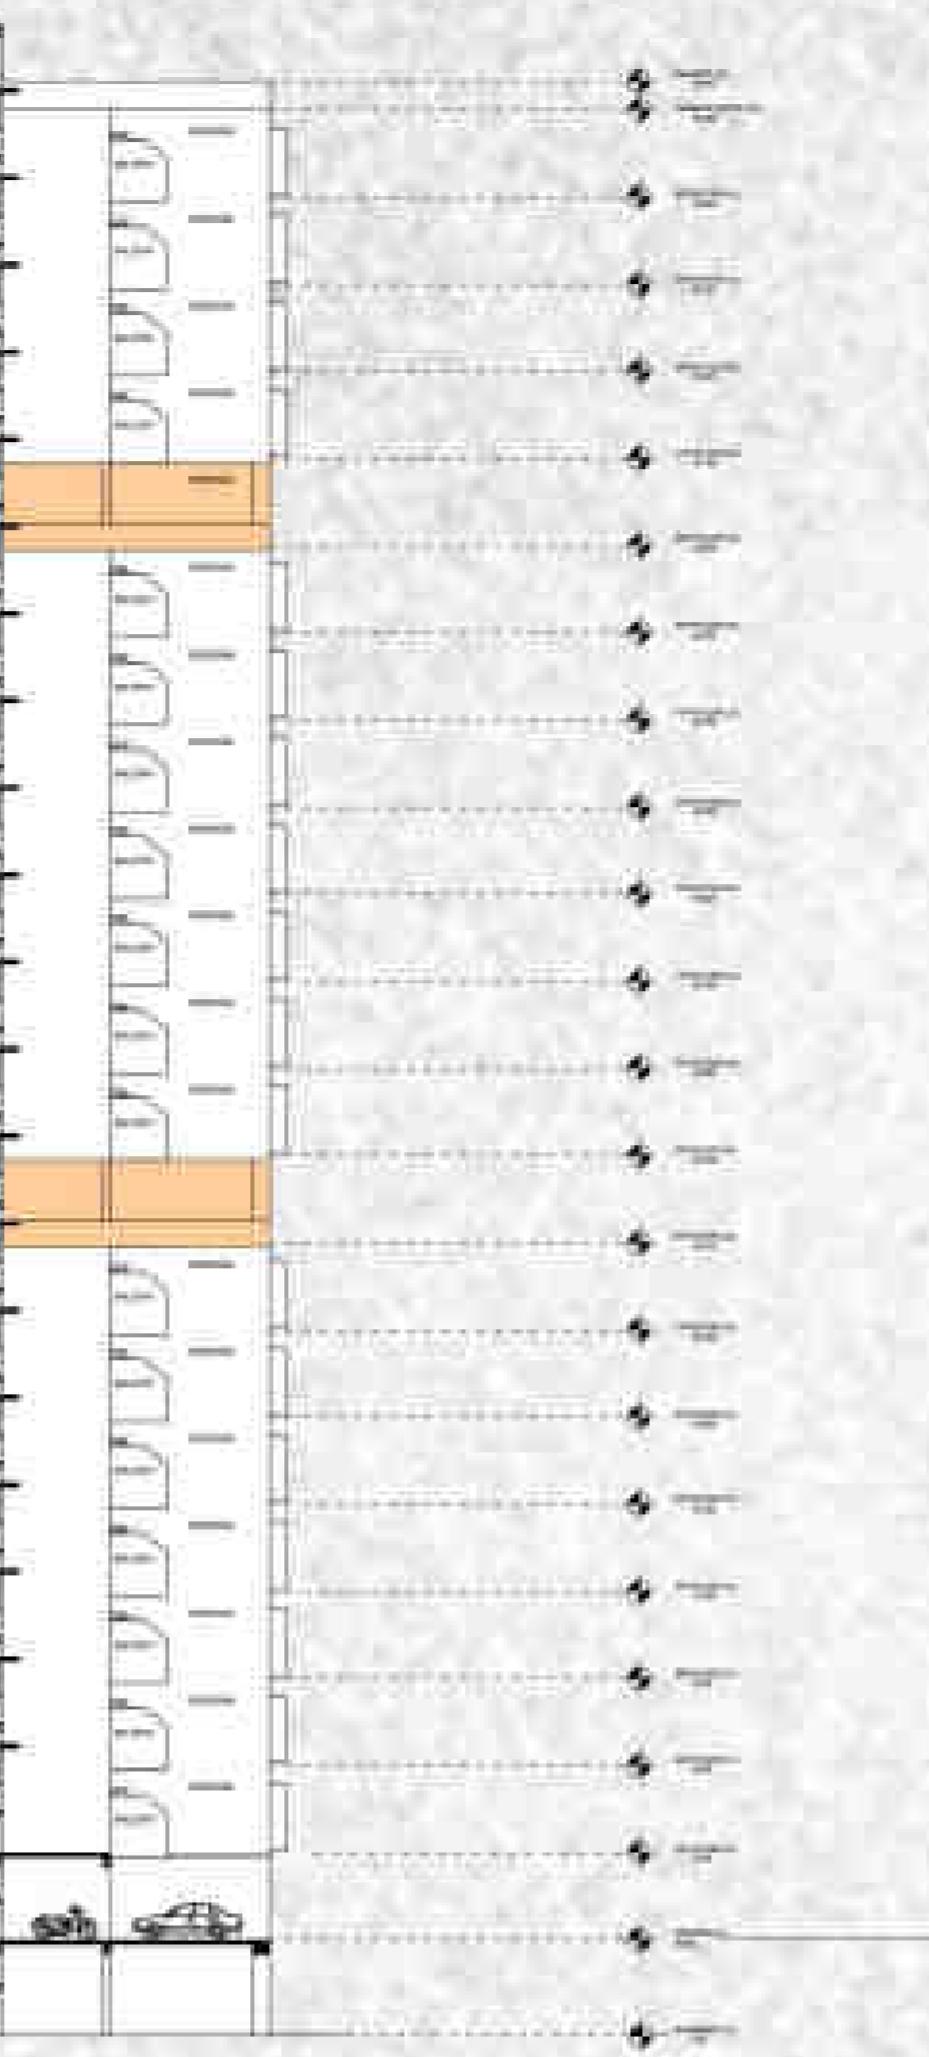







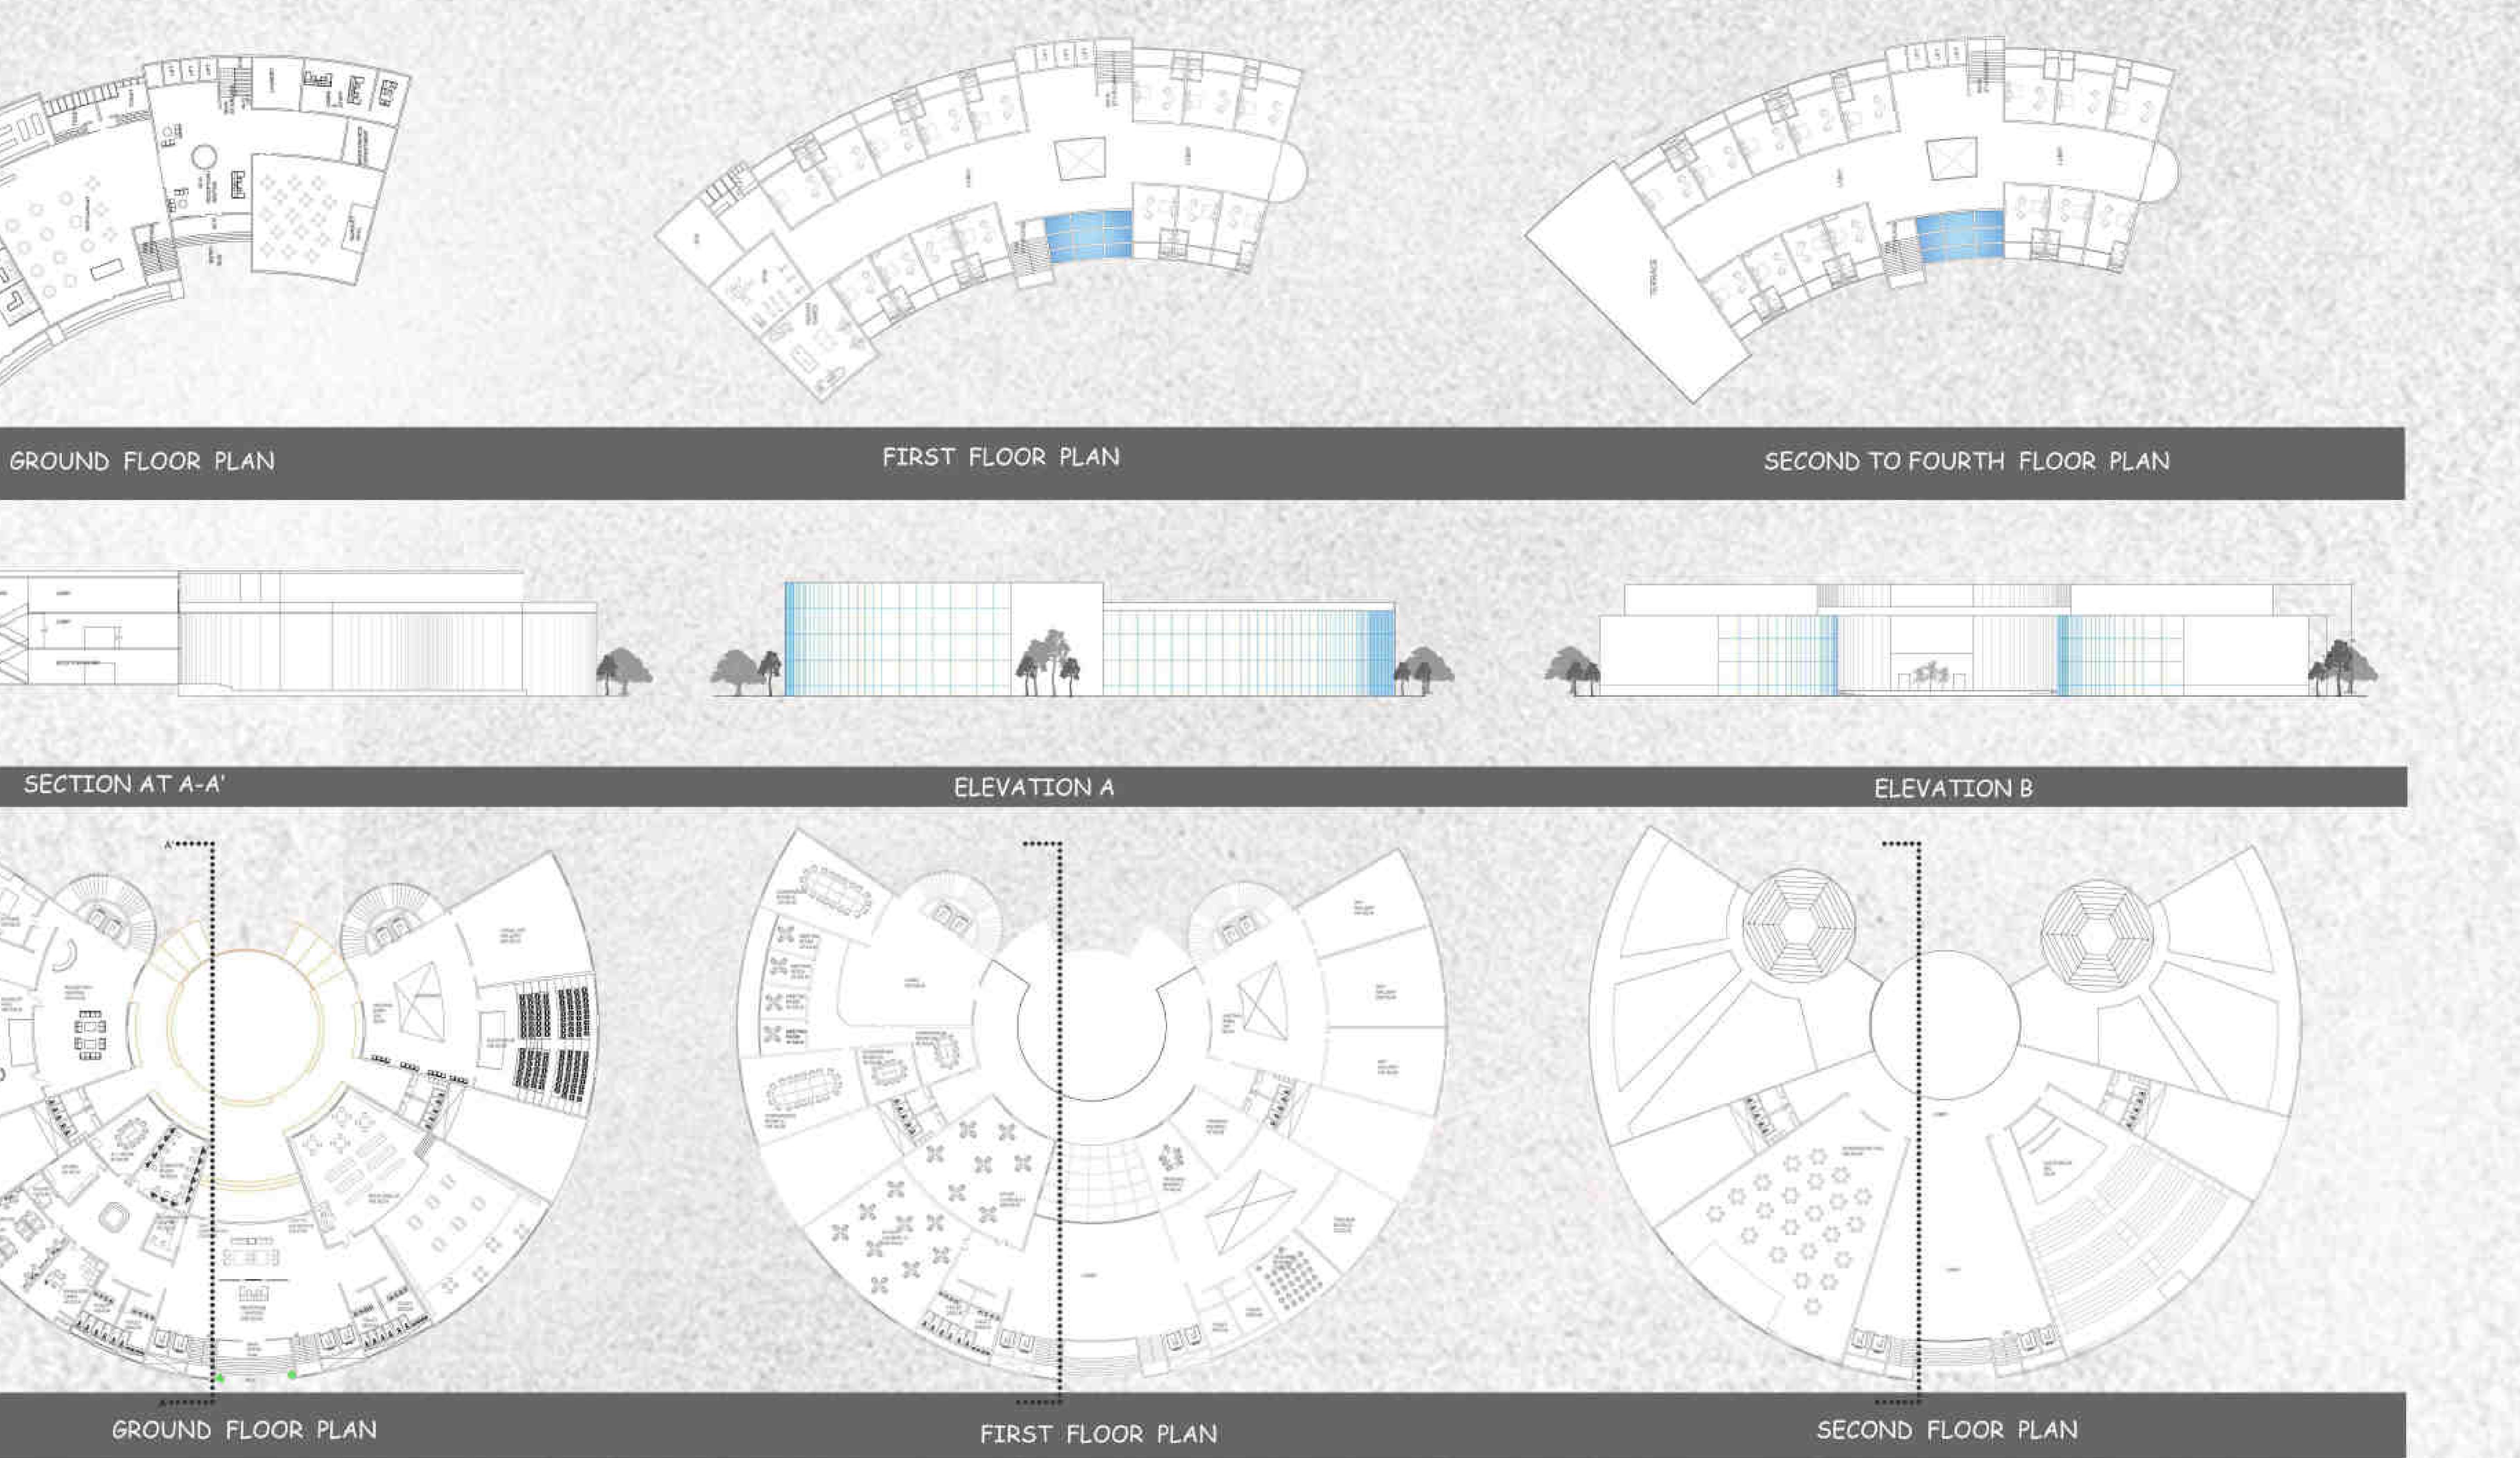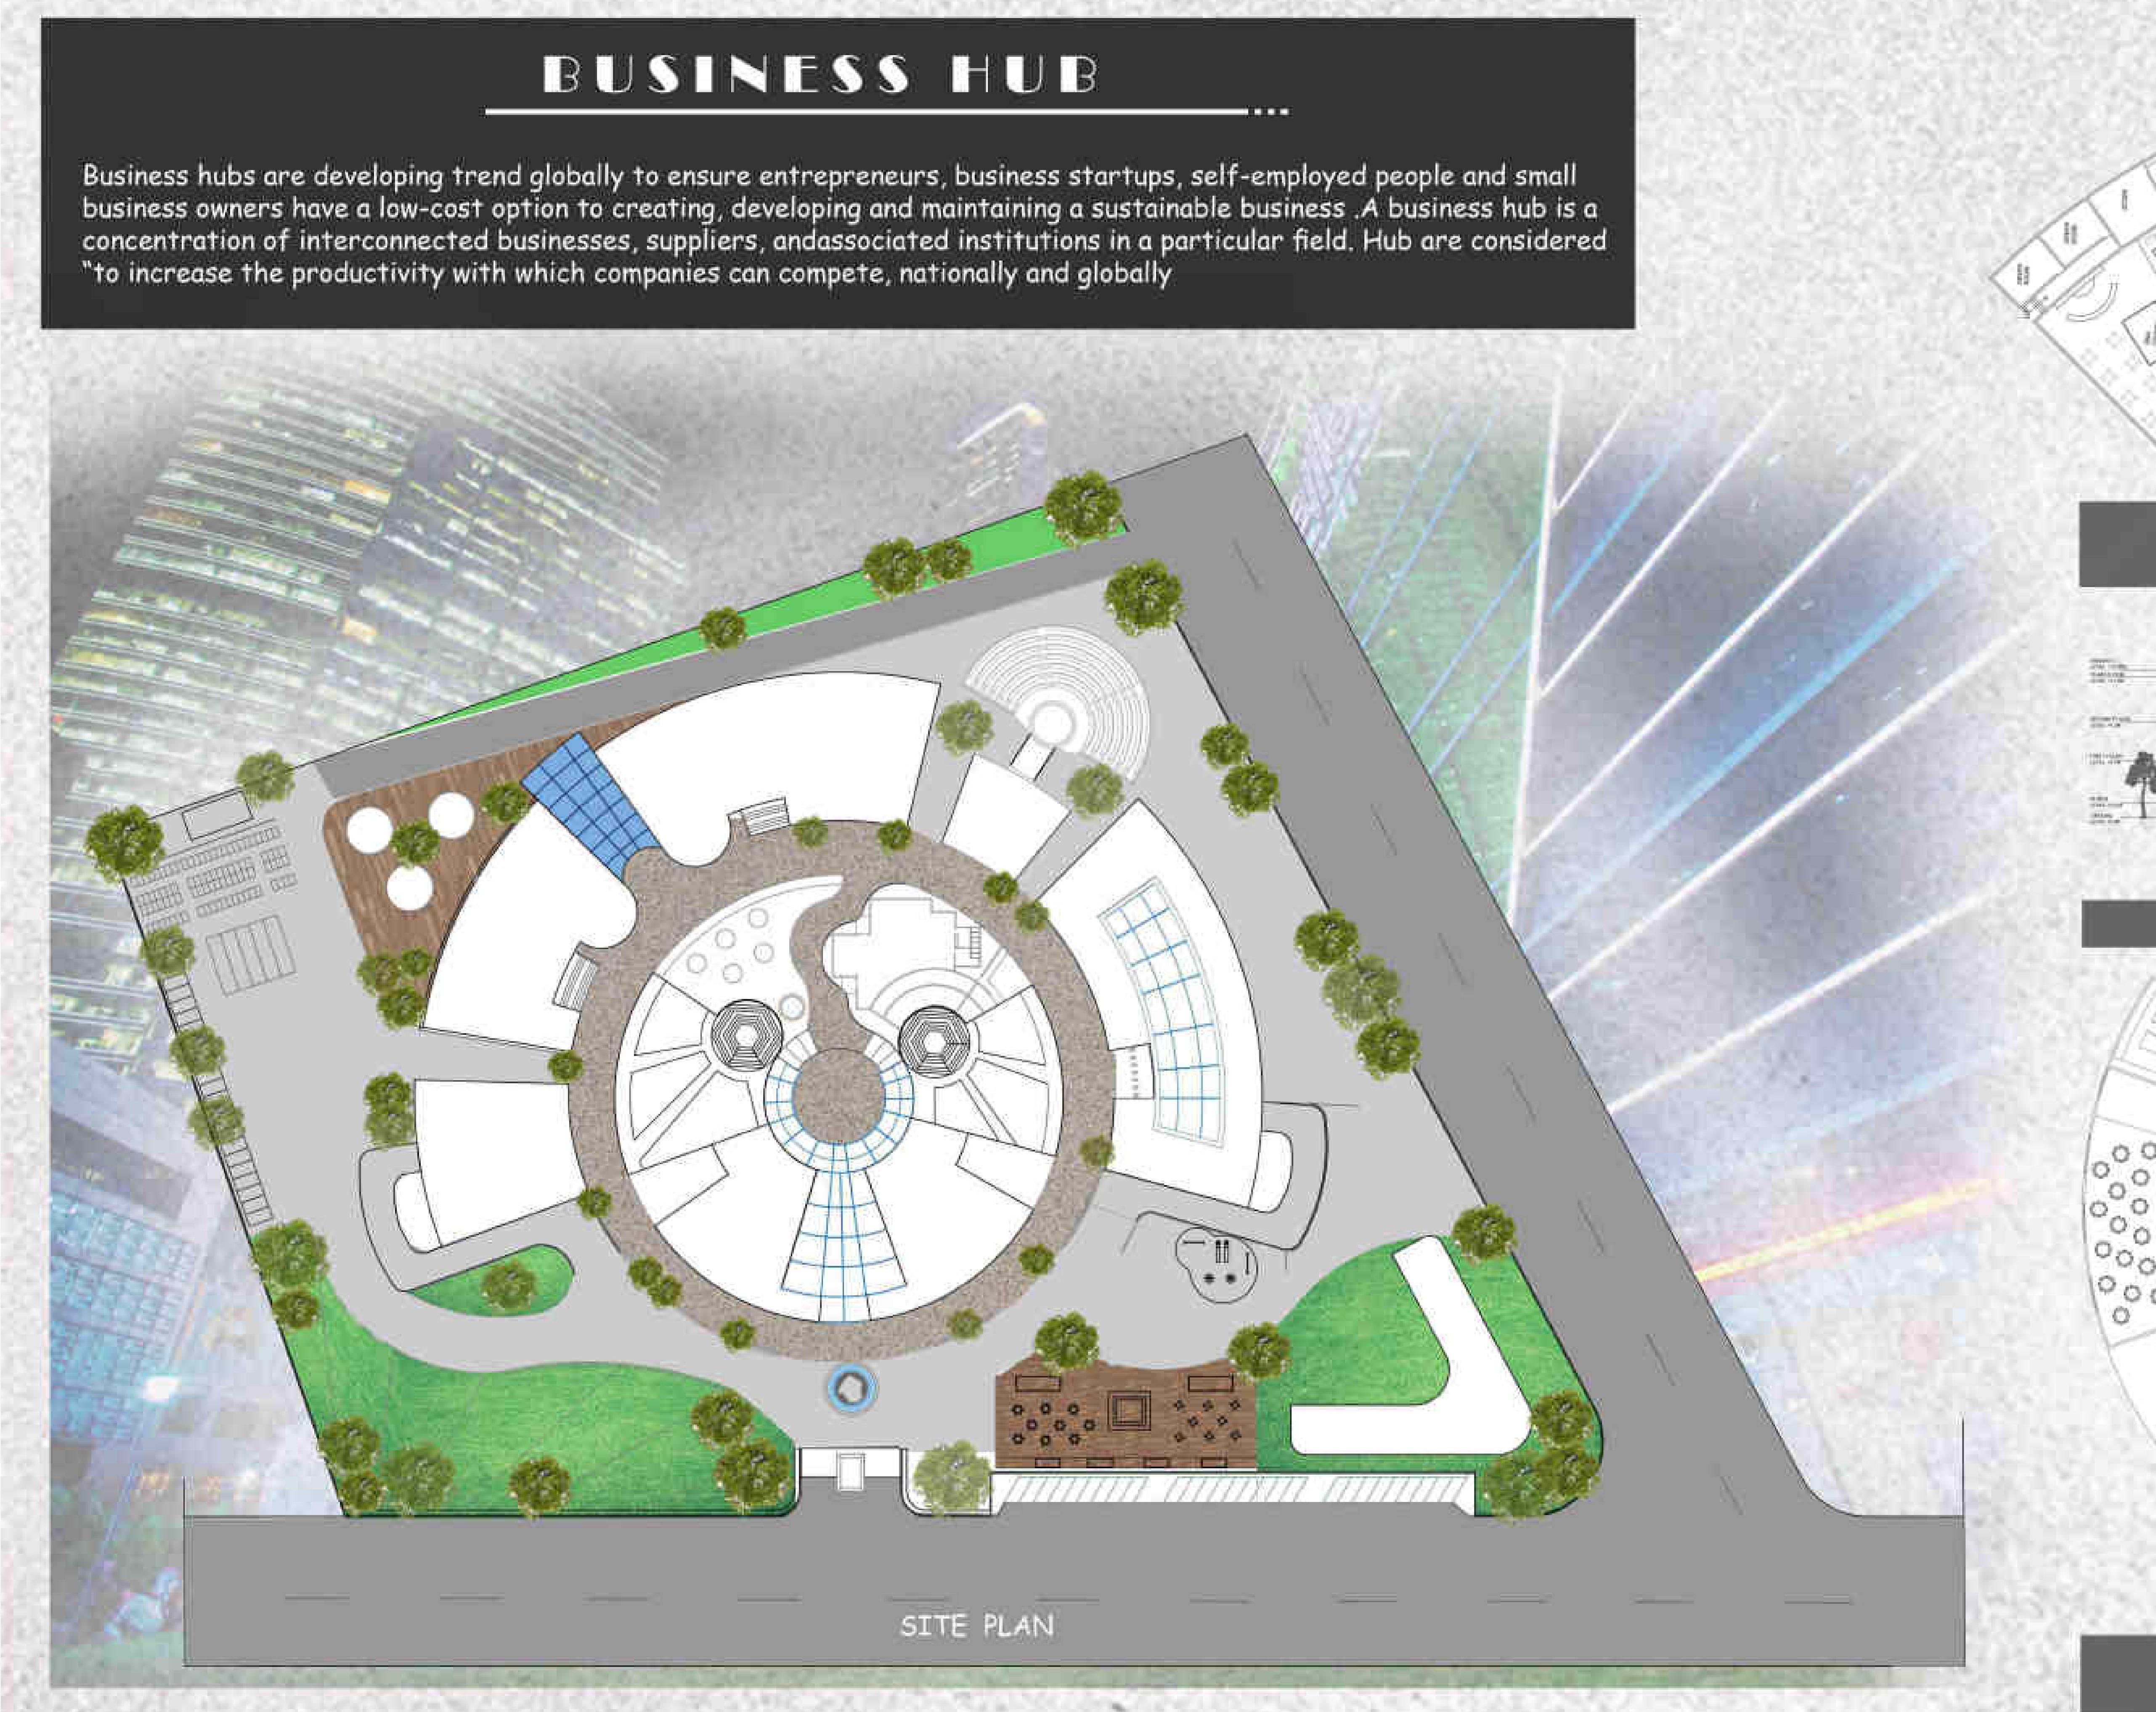

GROUND FLOOR PLAN

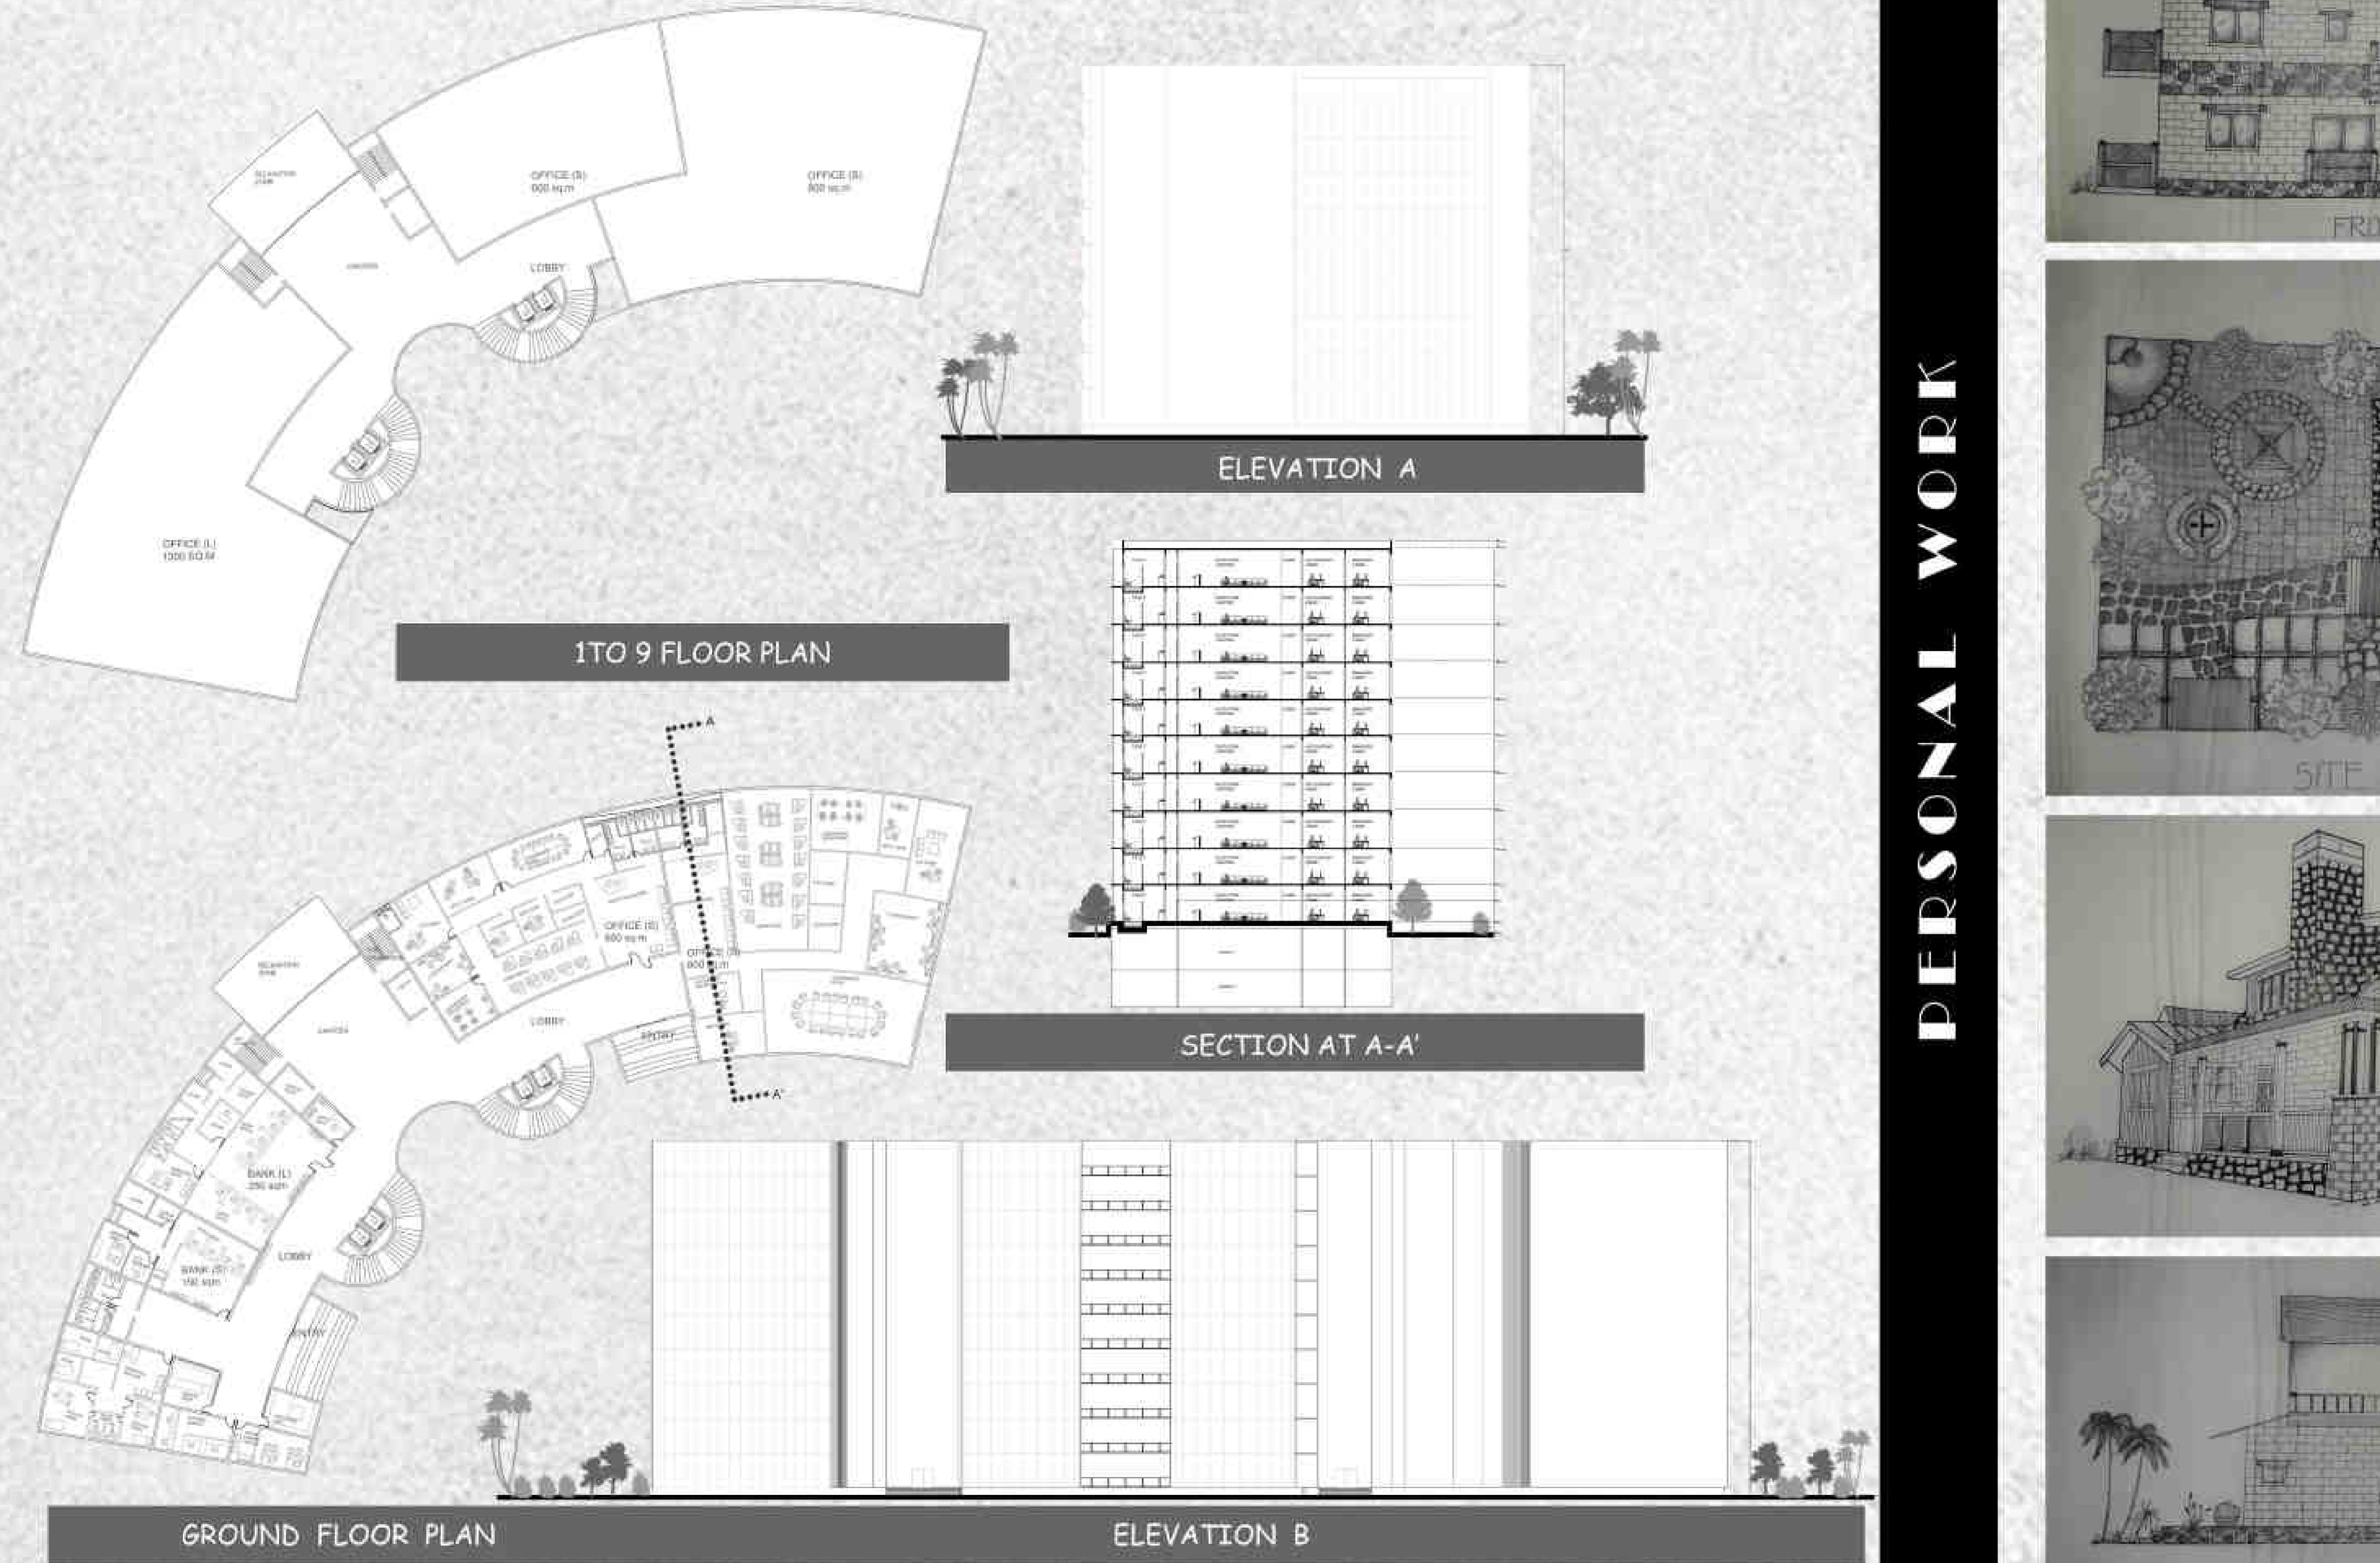

PERSONAL WORK

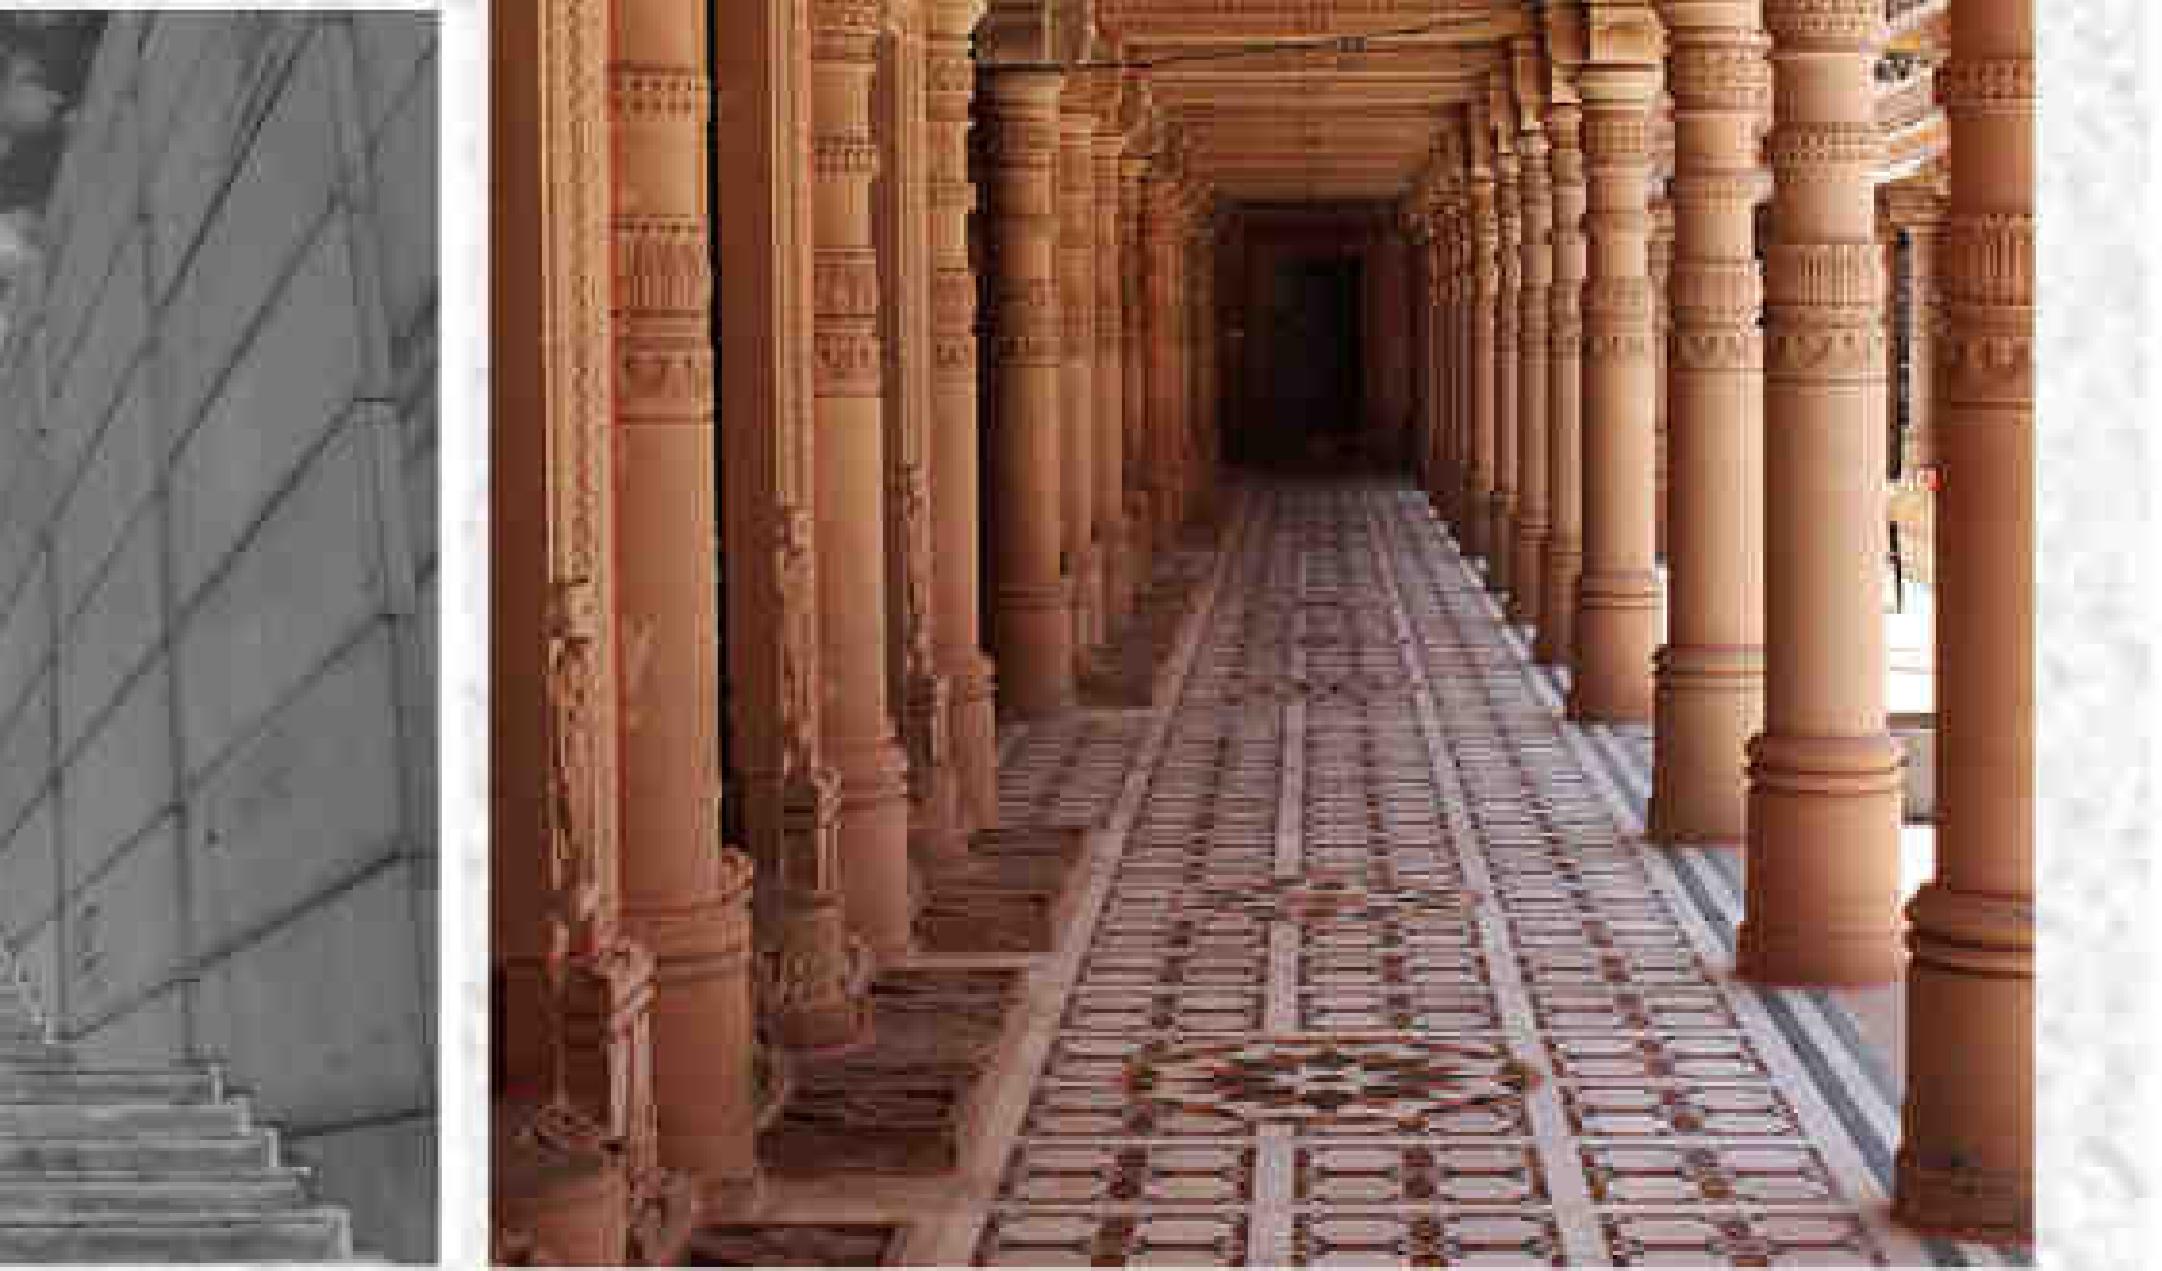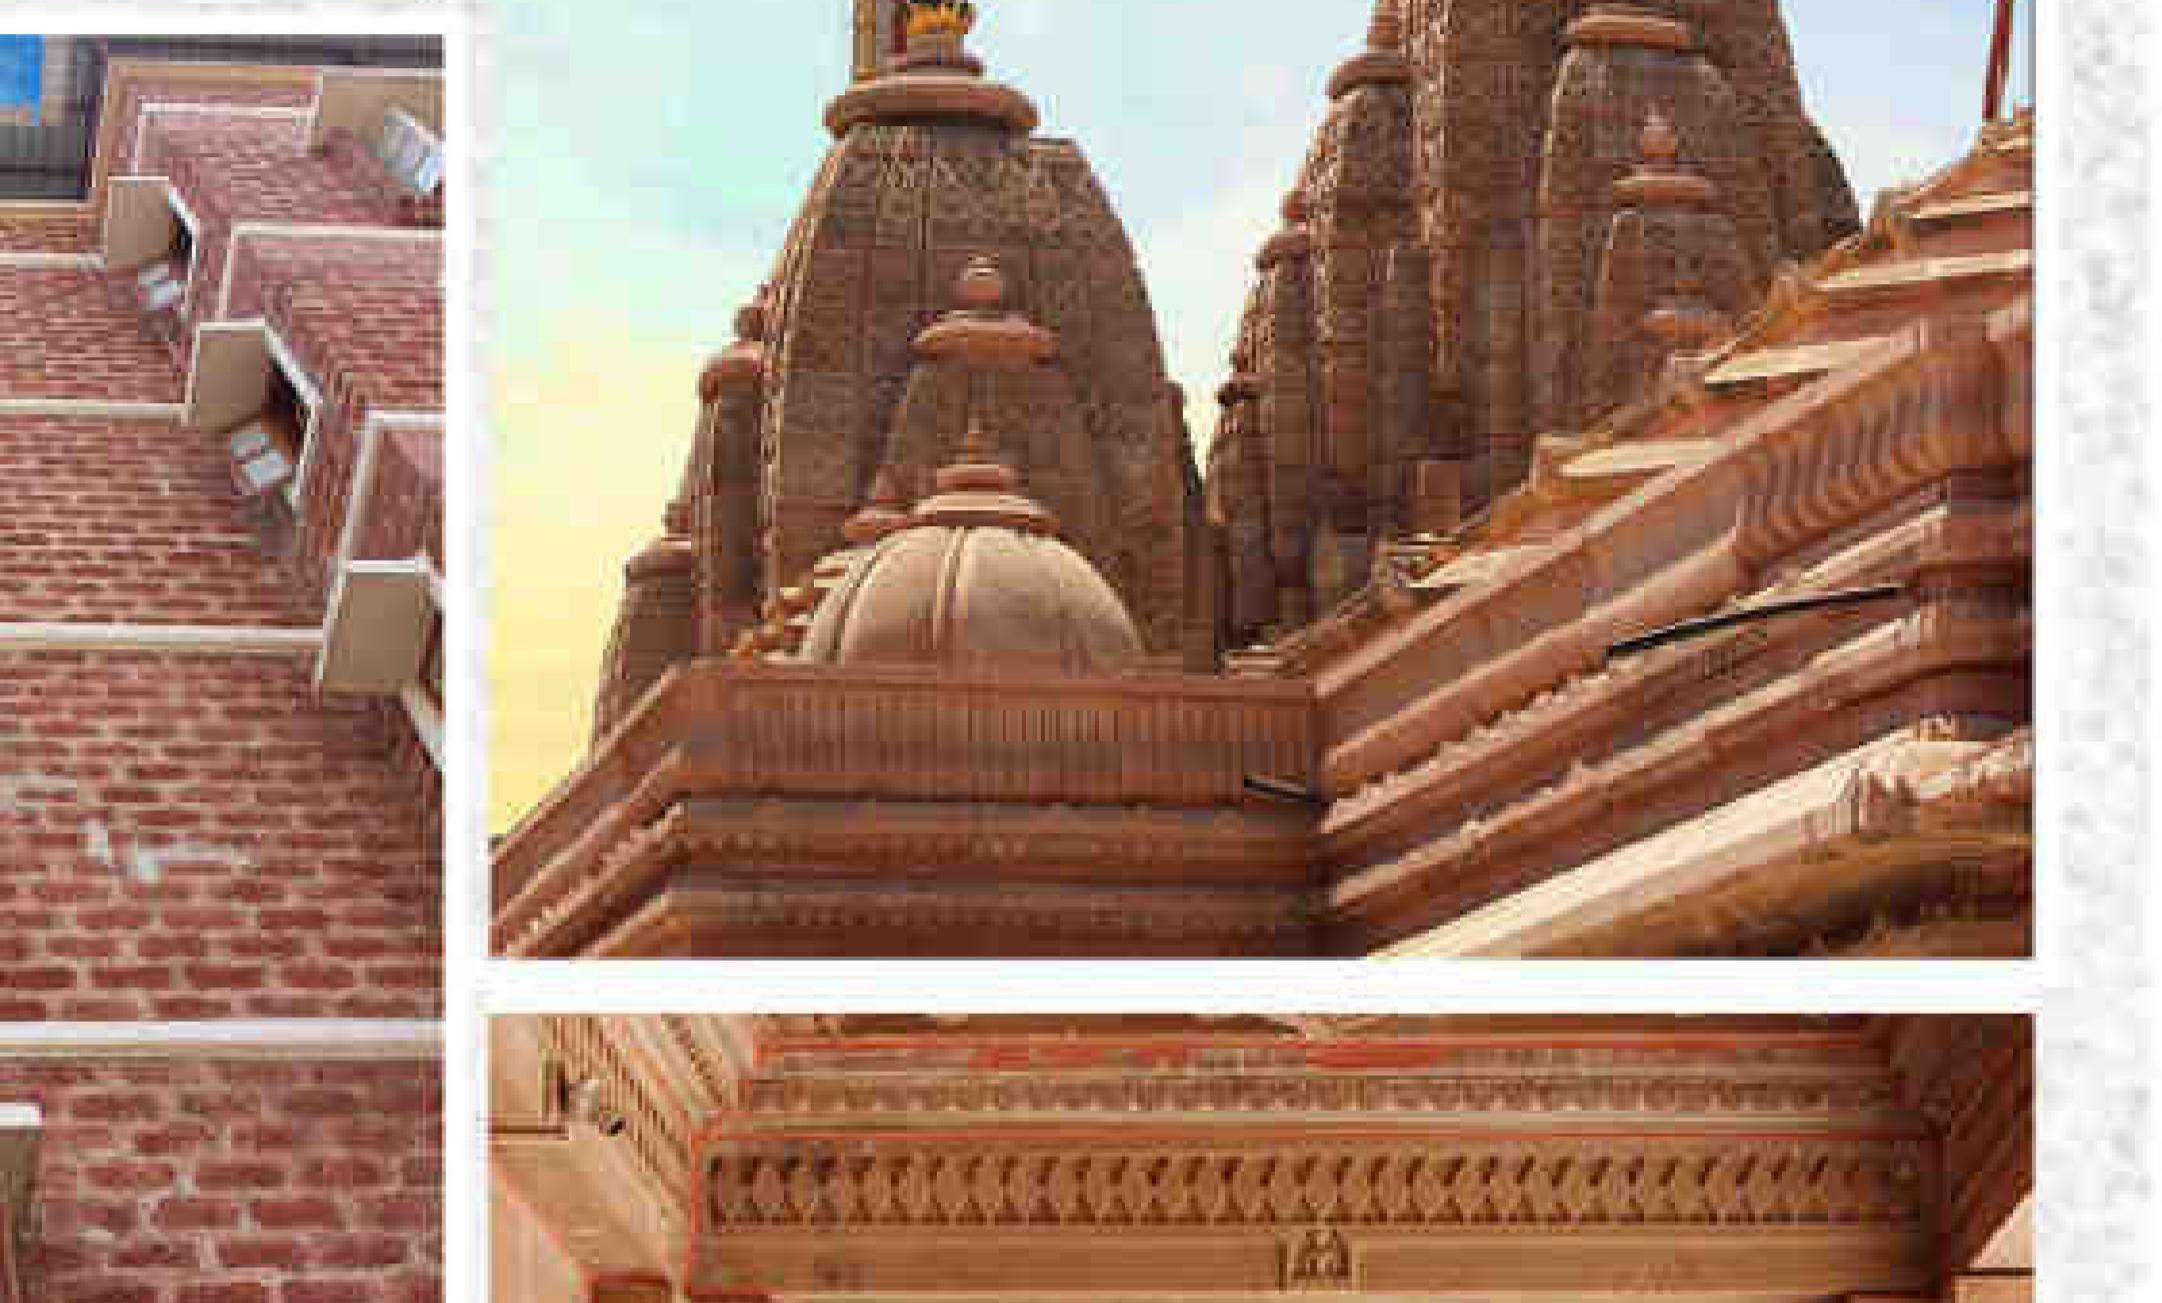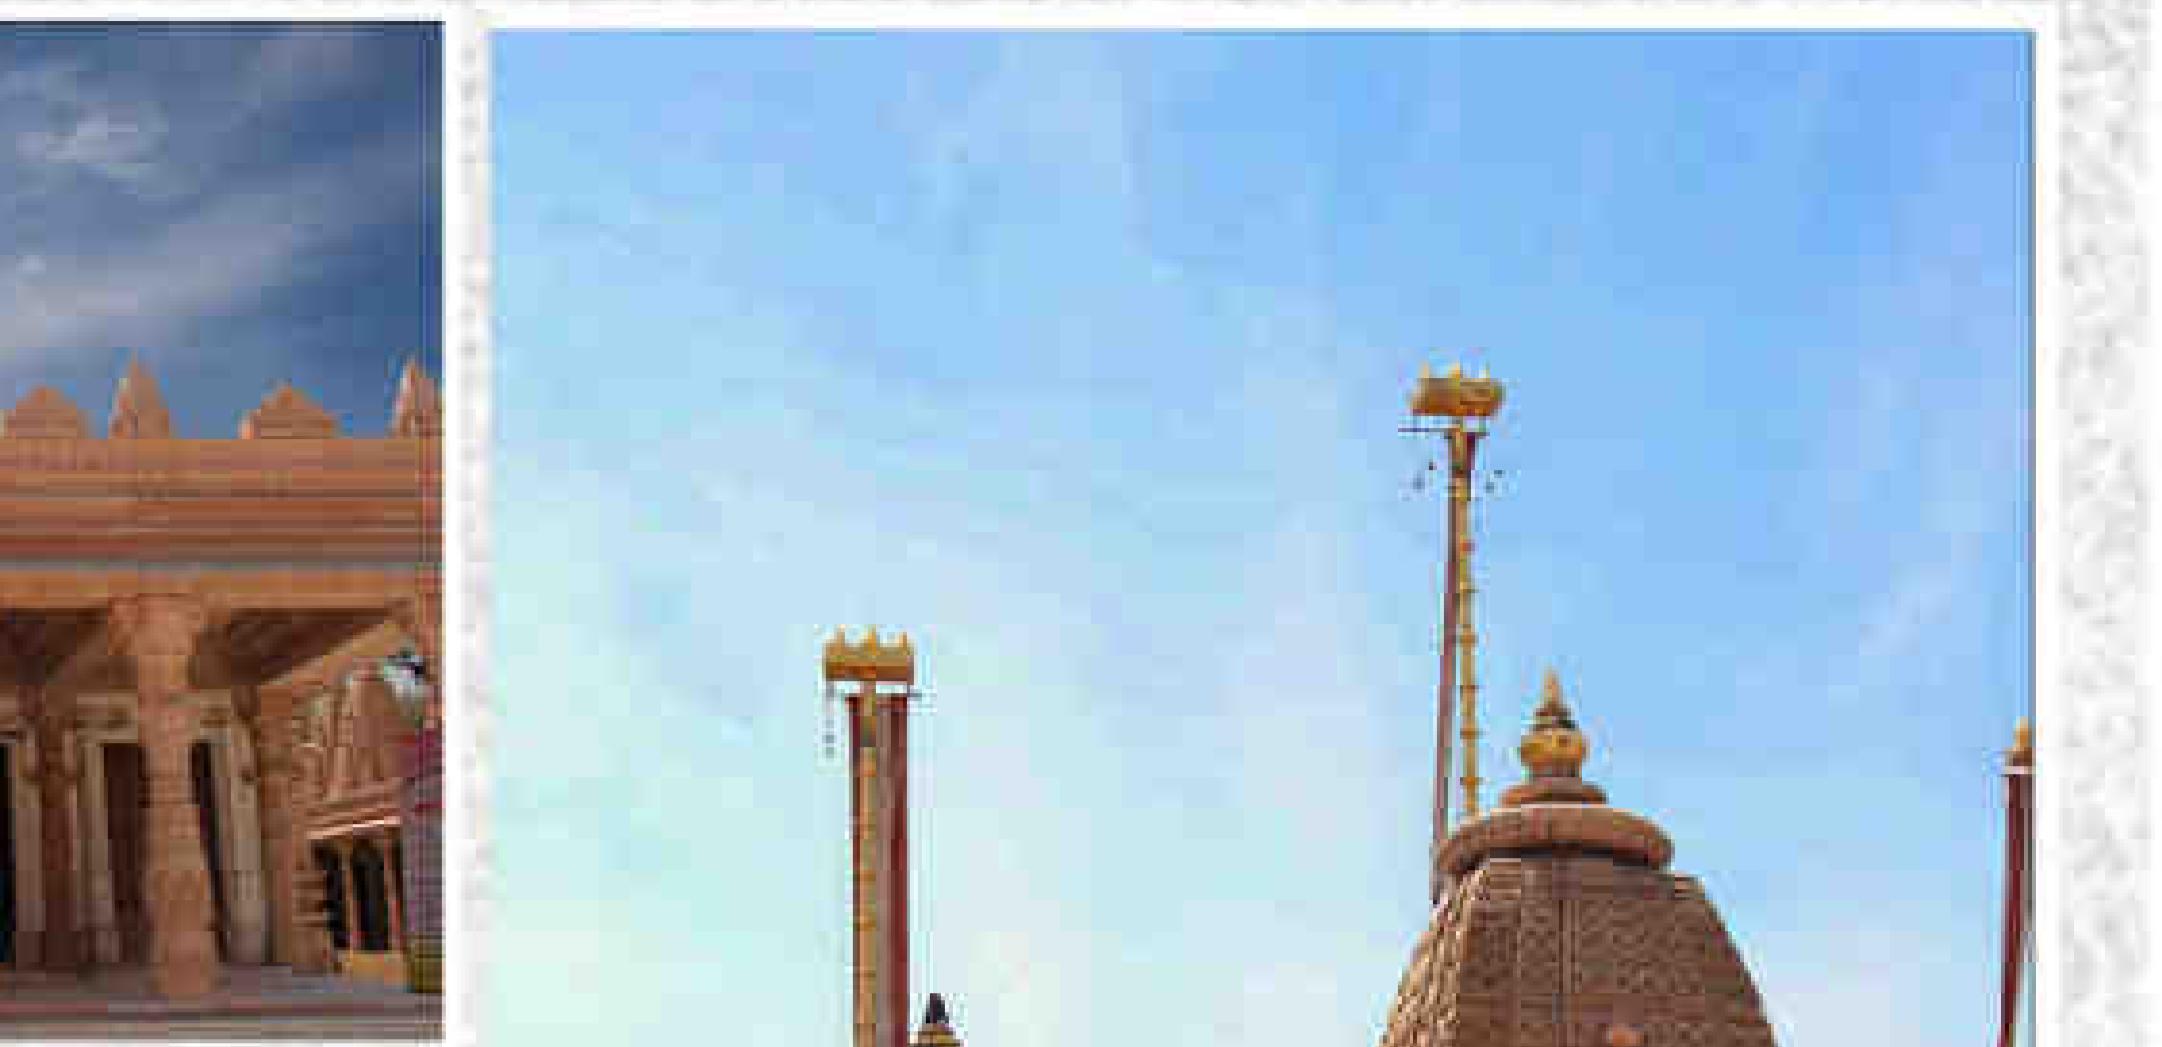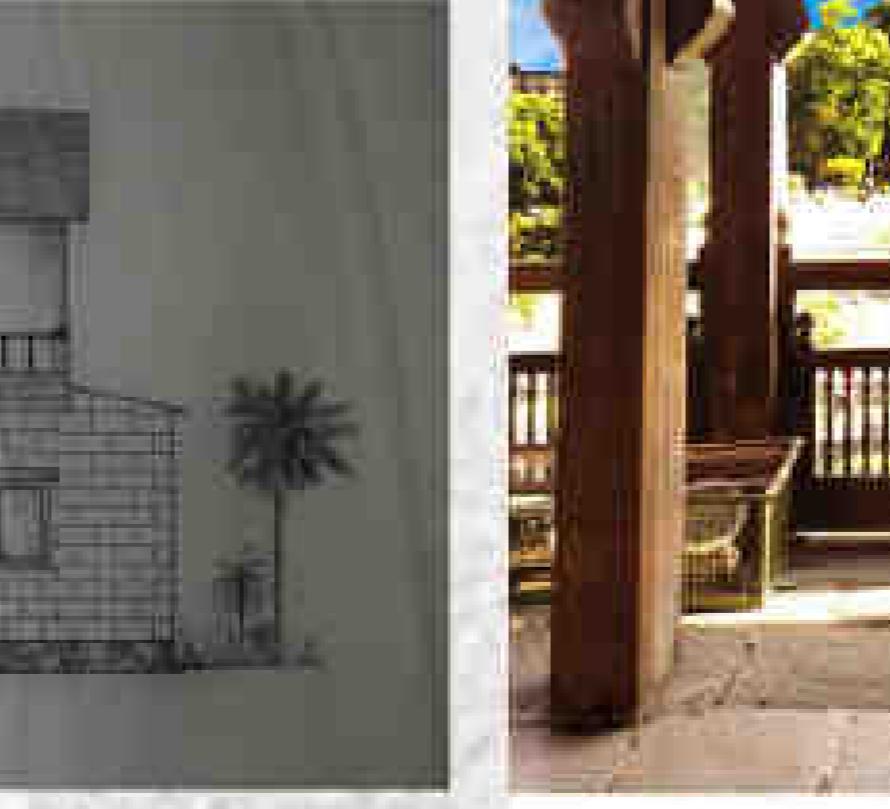

THESIS : **E**CO - **R**ESORT



ECO-RESORT


The Eco resort means it is built with local or recycled materials in a design that conforms to environment and harmonizes perfectly with the nature and cultural background of the place, relying on alternative energy.

An Eco-resort encourages the recycle of wastes and sewage water after treatment.

It is a space where human beings live with other creatures such as plants, birds and animals in an integrated, homogeneous and balanced manner.


It is accommodation that has made important environmental improvements to its structure in order to minimize its impact on the environment.

Eco resorts are mostly presented because of their locations, often in jungles, and their design inspired by the use of traditional building methods applied with the skilled local craftsman in areas.

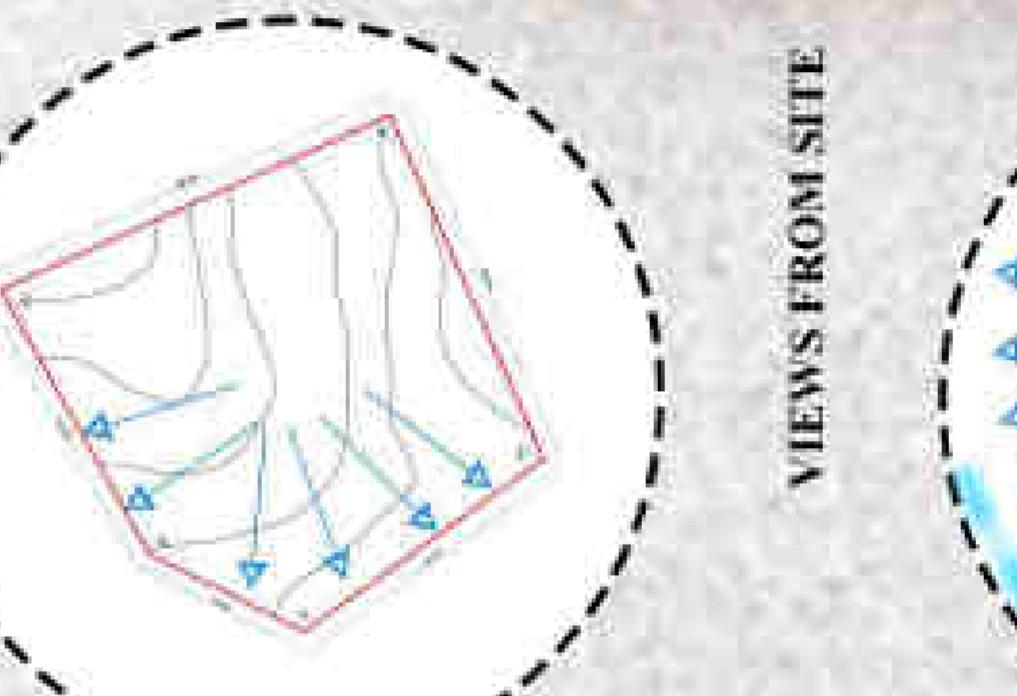

TOTAL SITE AREA
35,200SQM
ACRE - 8.7

SITE ANALYSIS

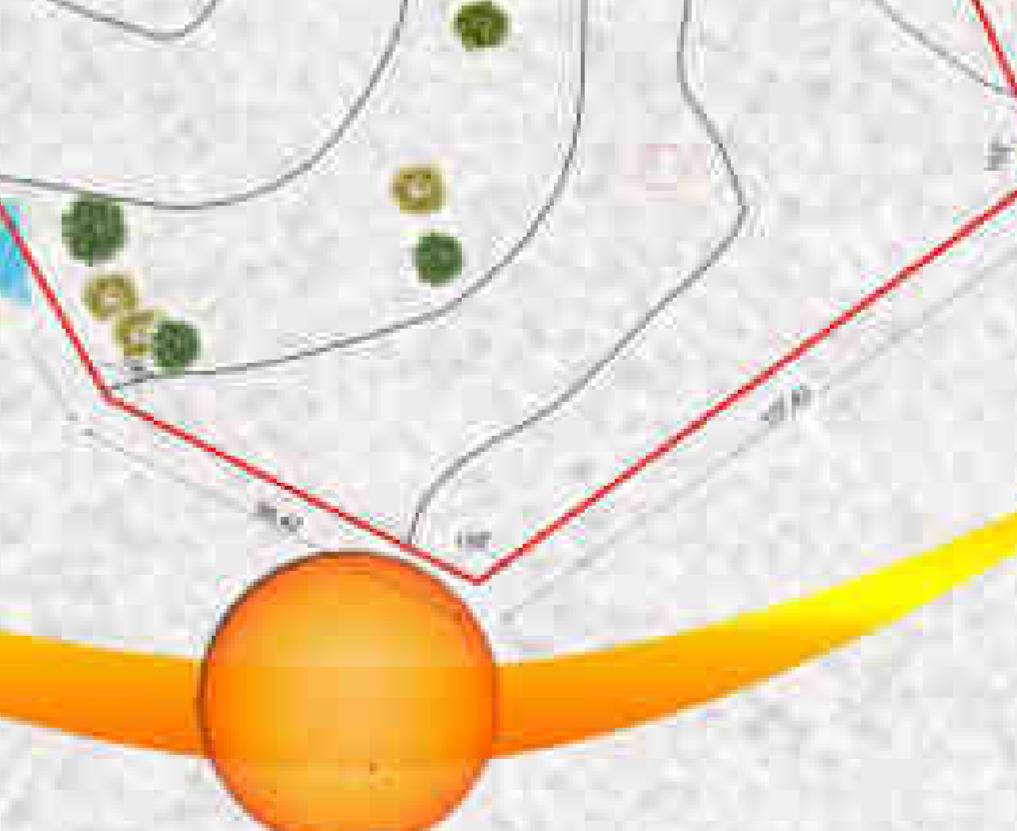

Site has a very good climatic conditions throughout the year like another hill station. During the rainy season best scene can enjoy from the site.


Topola is located near to the Mahabaleshwar. It is situated away from the crowded areas, so its location would be perfect for the Eco Resort.



Site has terraces having slope facing east-west direction. The terraces on the site beautify the site. Farming is done across the slope and is one of the best methods.

The resort is designed as it emanating from the central spine of the plant as a main walkway and radiates like its leaves with different sizes and its own shades. Water is the one of the main source for its growth so when we watered the plant just like the movement of the water droplets on the leaf, so as the circulation of people across the site. The main circulation walkways and pathways have a strong bold main axial stem which defines flowing movement.


Flamboyant forms of the circulation network coming with the tree plantation along the pathways create suspense as we move. Also it breaks down the long walkways, into minor segments of different characters. The hierarchical framework help us to encourage the visitors to walk a resonable distance to ensure healthy days life at the place.

CONCEPT

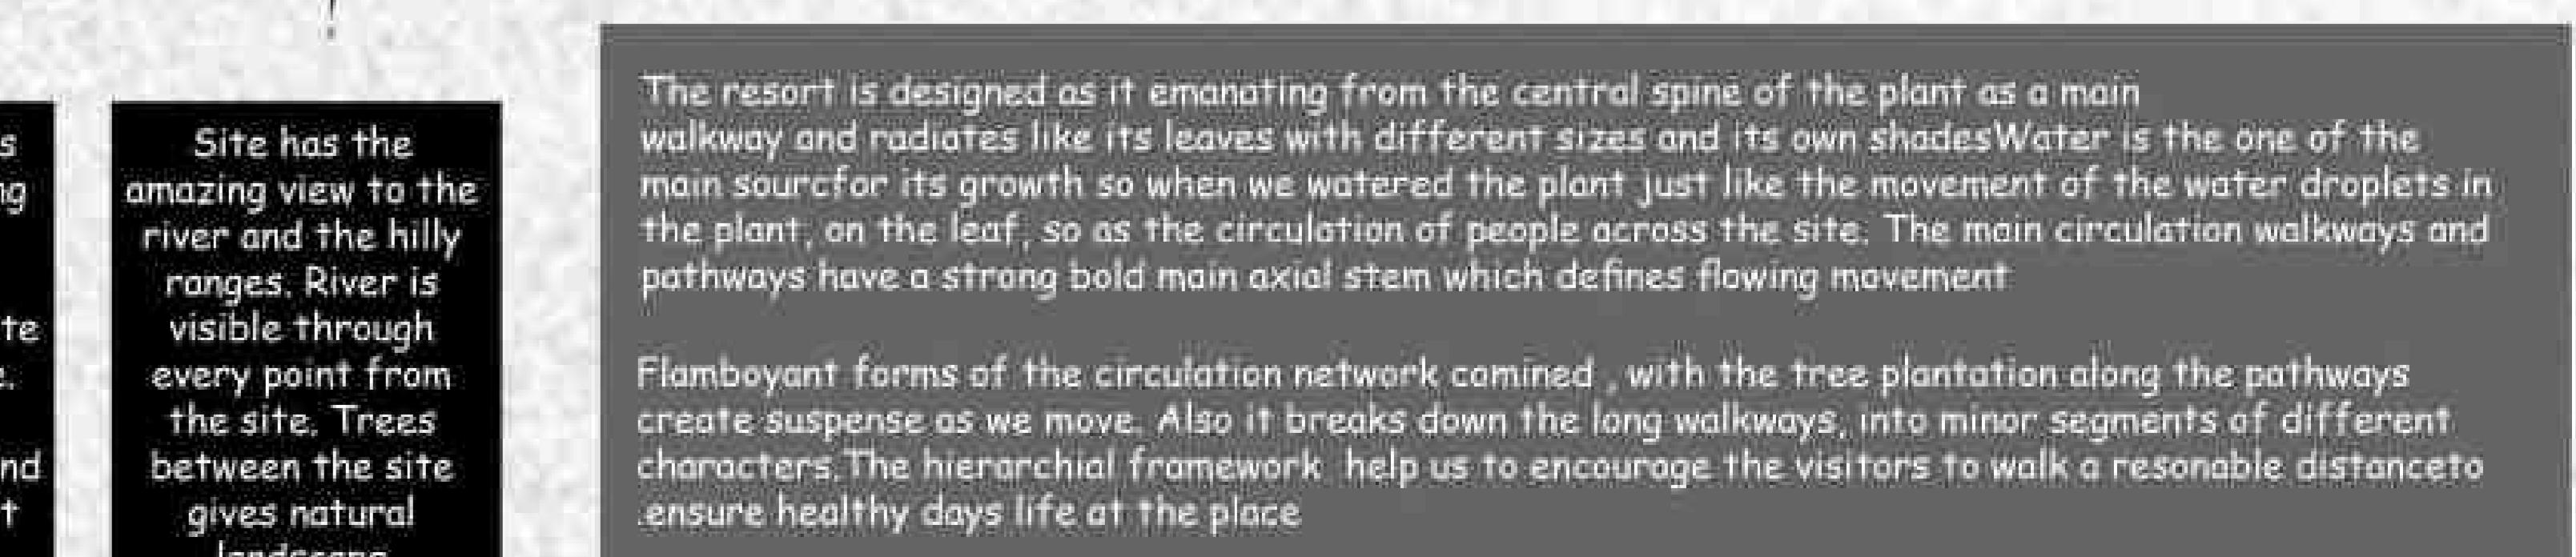

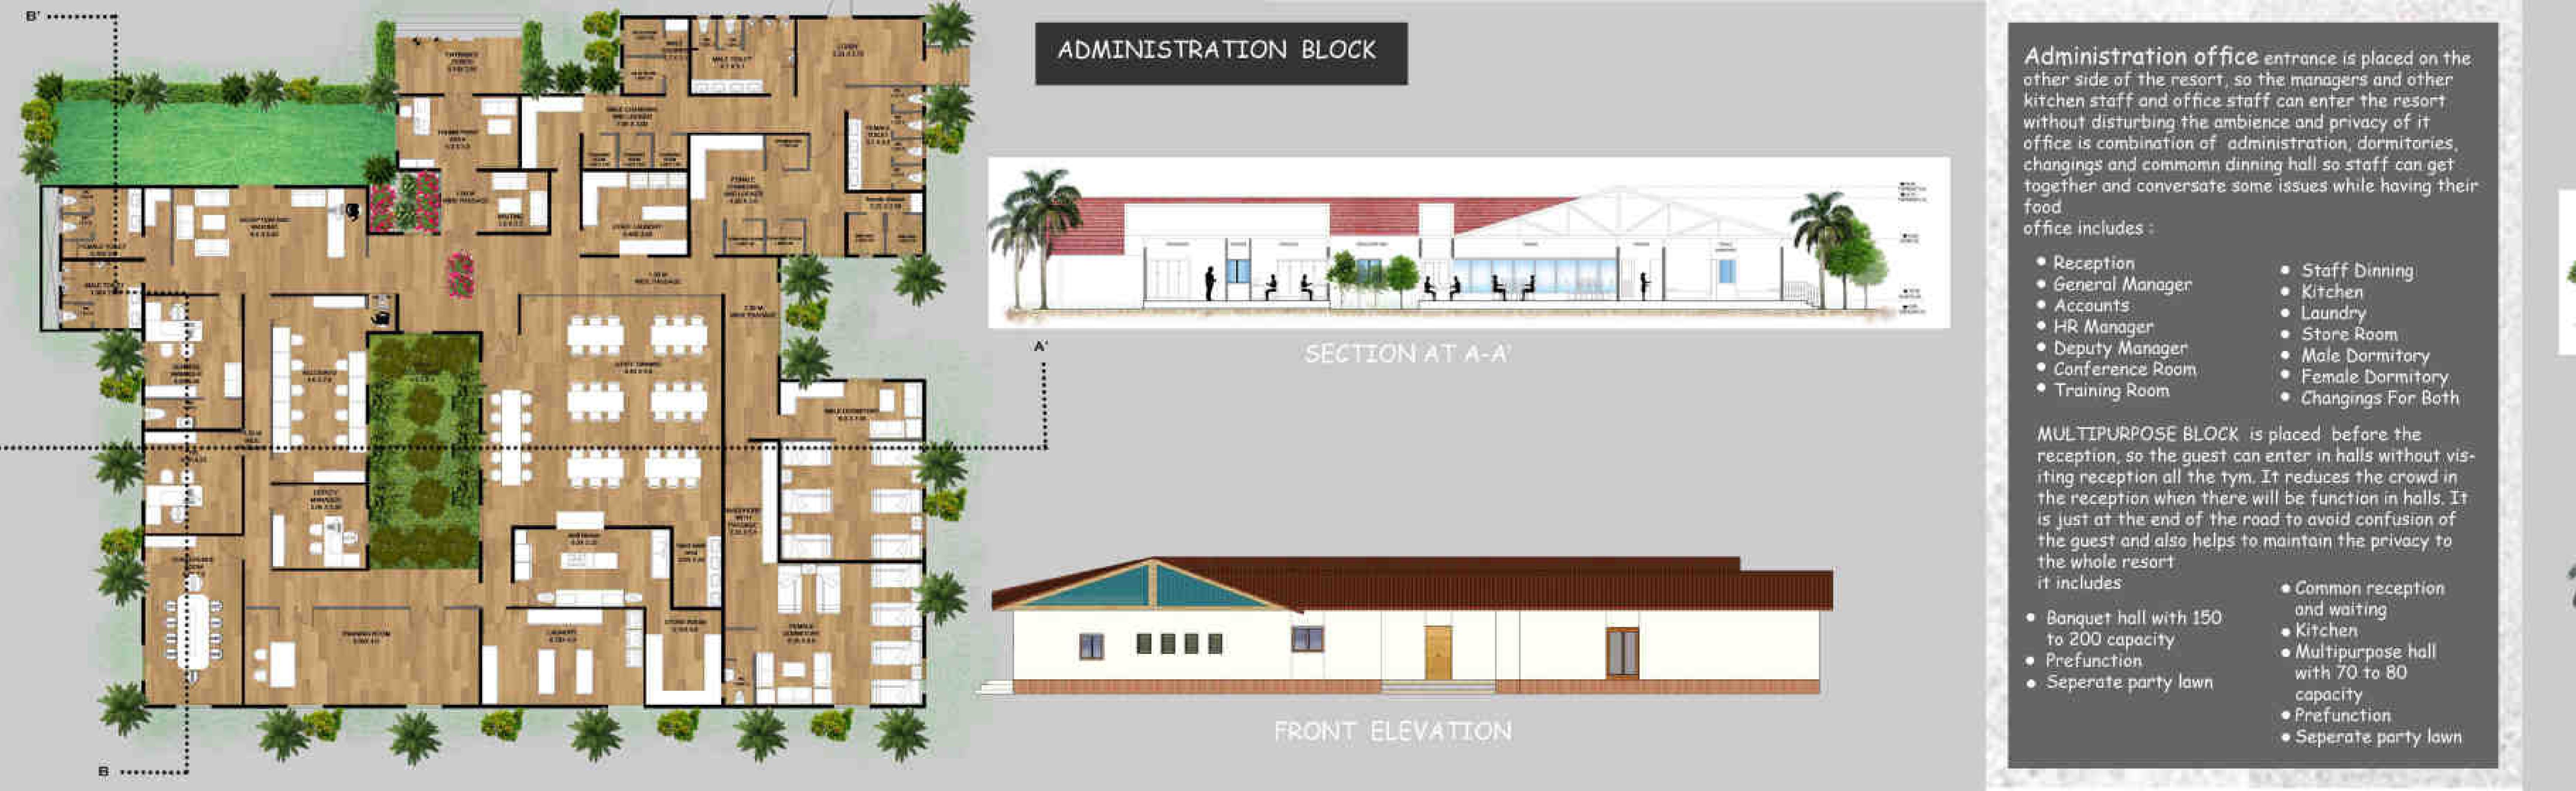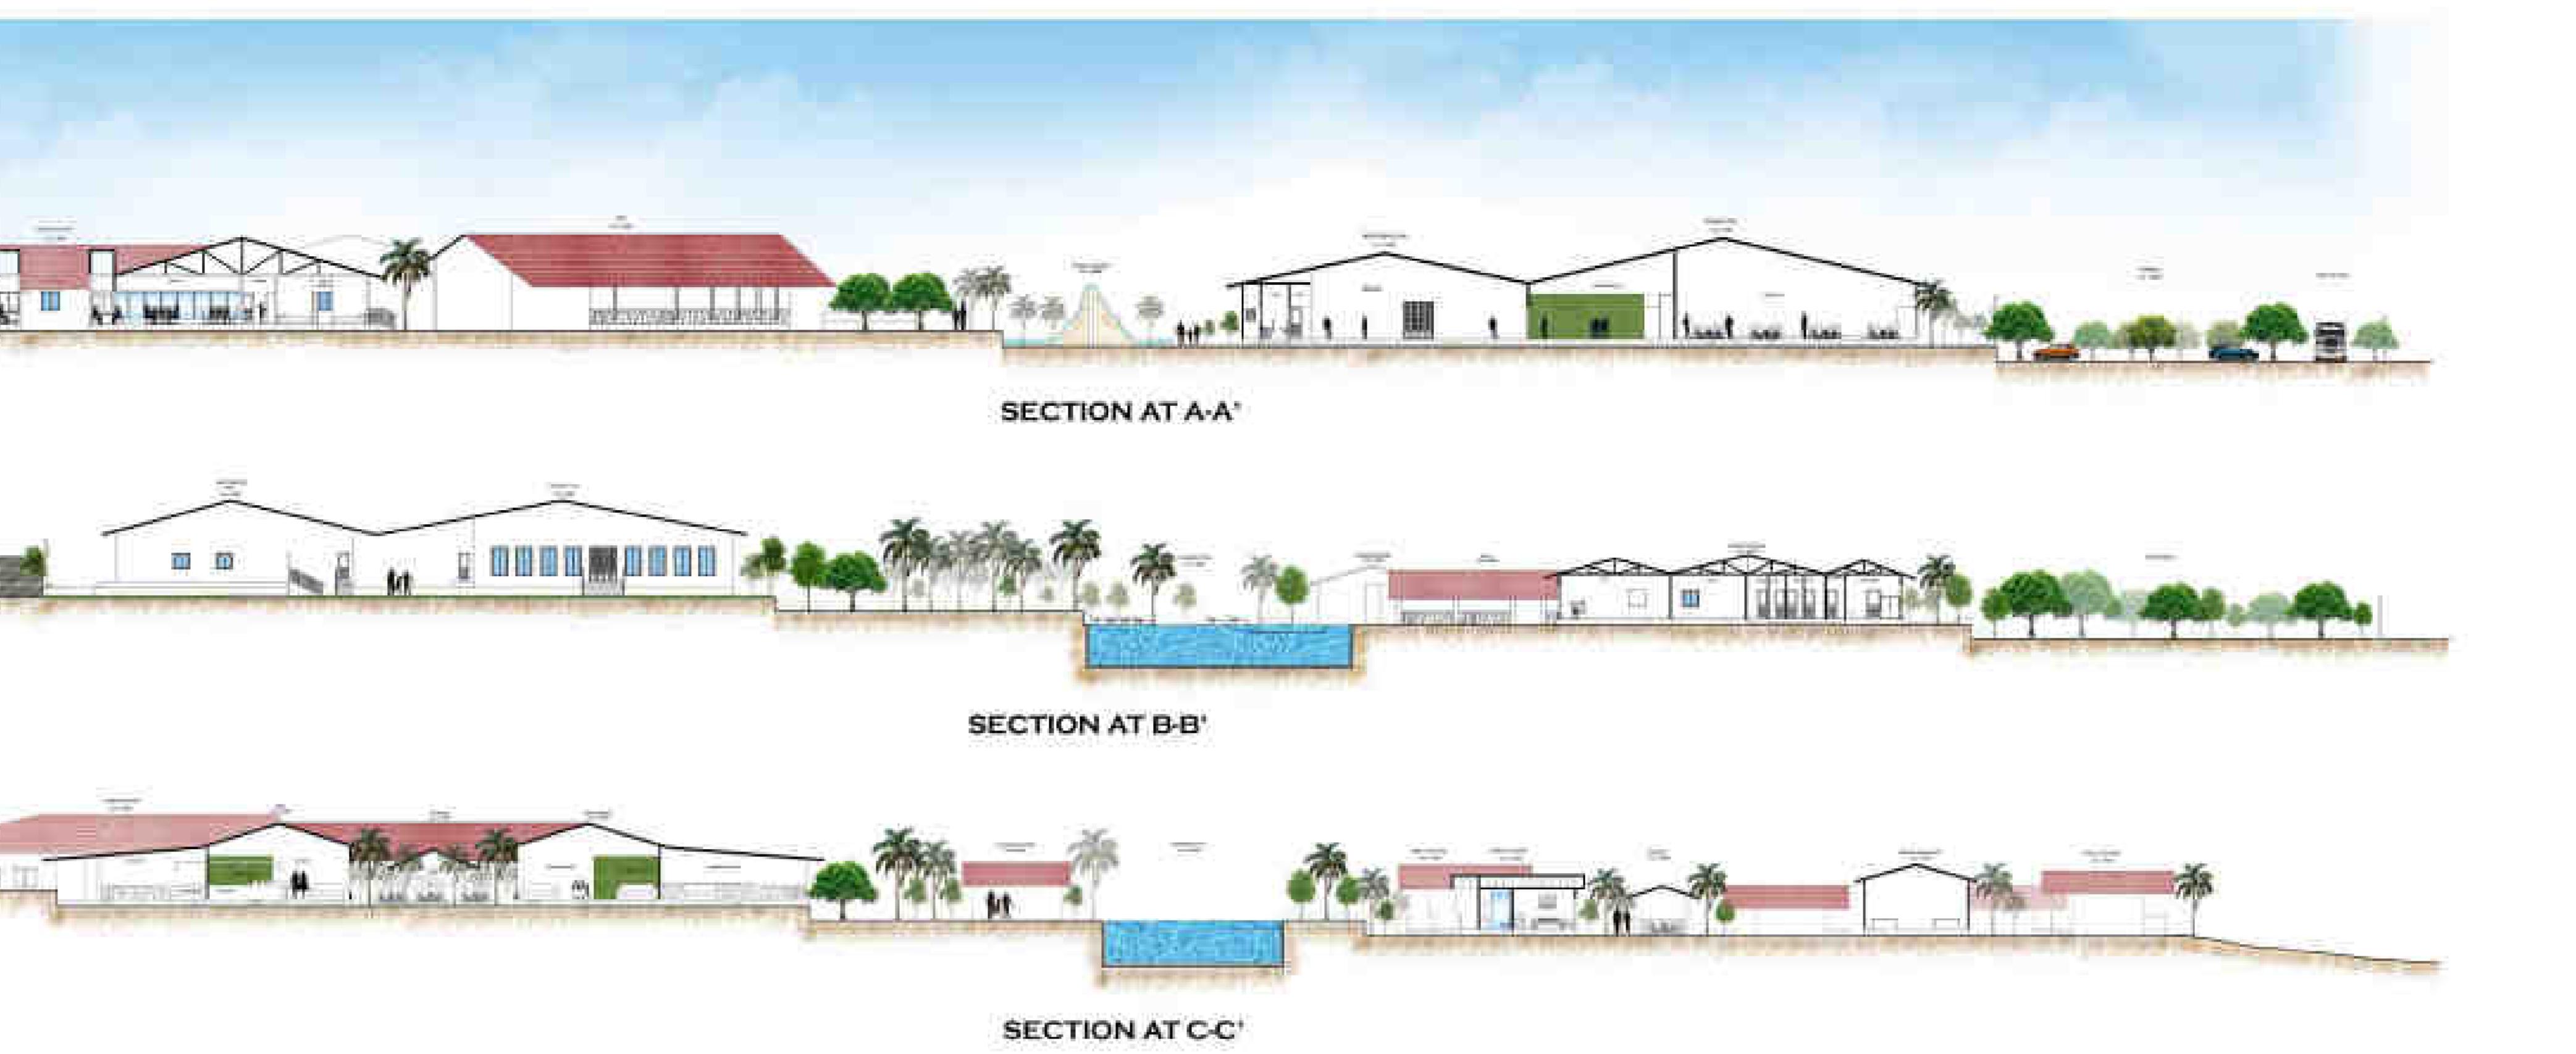



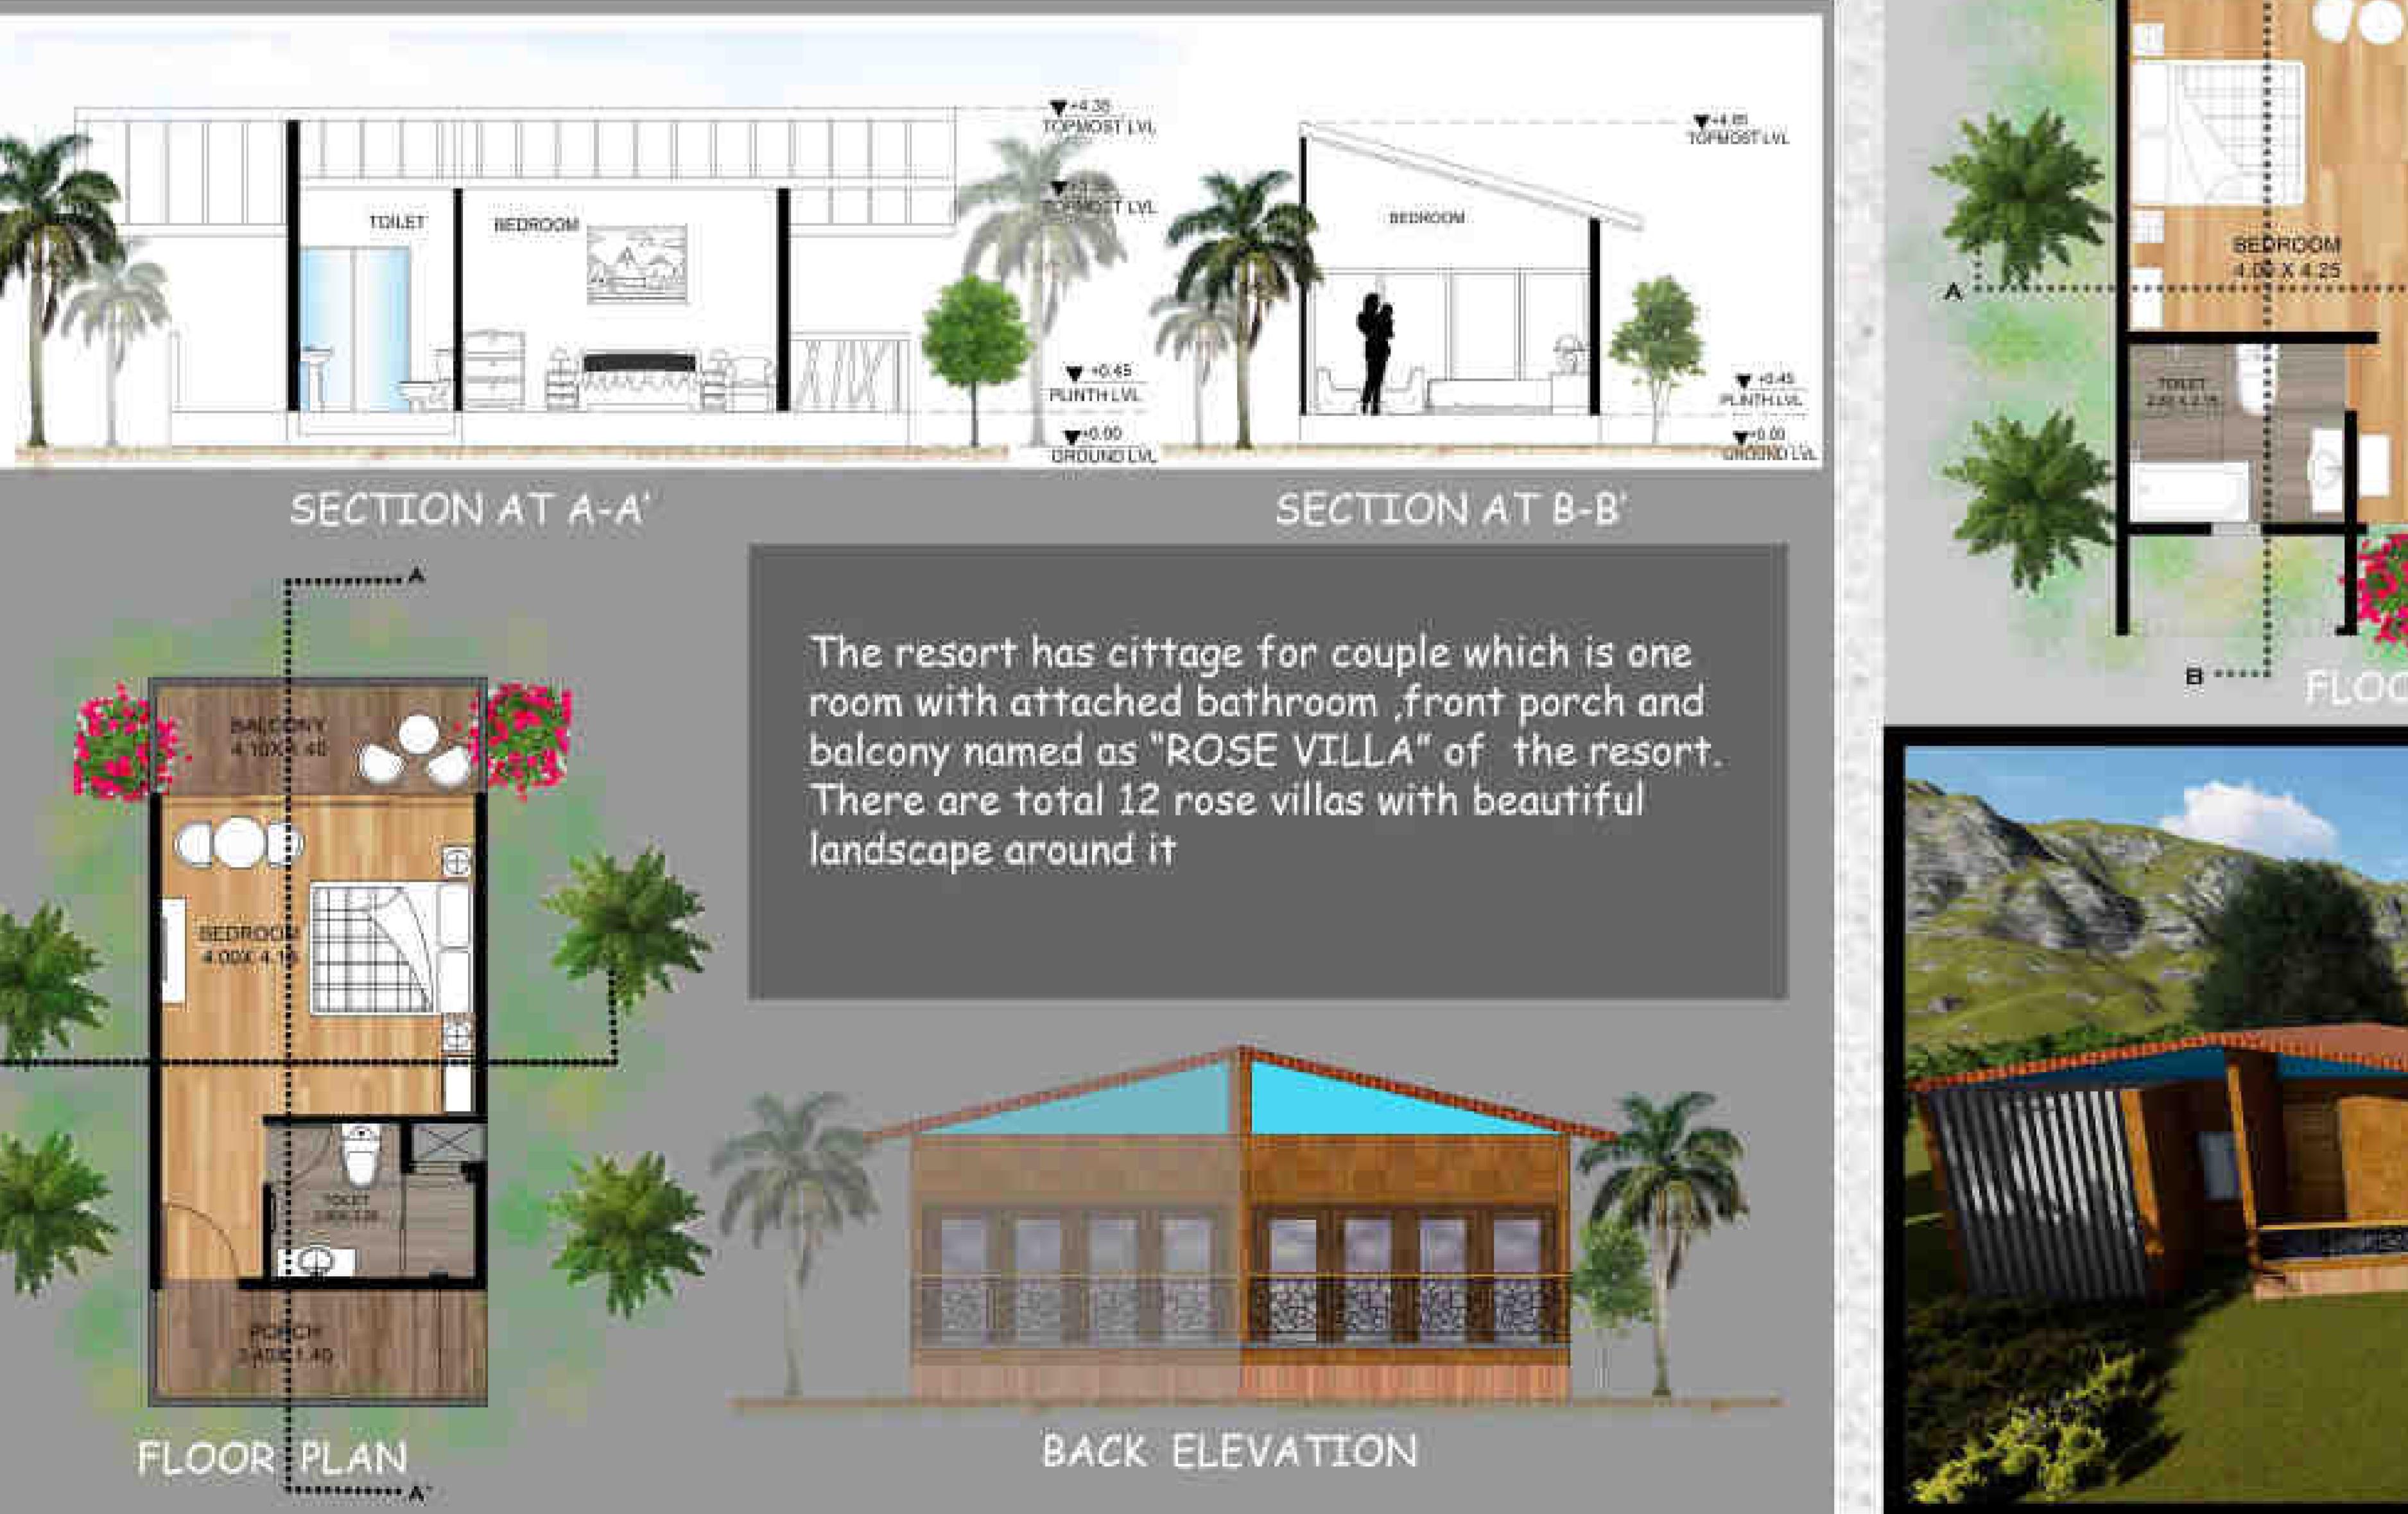

villa is named as "BOUGANVILLA" which has two master bedrooms with one toilet. It also has front porch and balcony. Villas has private lawn in the back-yard which is surrounded by locally found flowering trees and specially bougainvillea trees. There are total 9 bouganvillas which placed at the corner of the site for the privacy, additionally villa has great mountain view from he balcony




Third villa is "LOTUS VILLA" which has spacious ground and upper floor with privatefacilties. It is specially designed for family and placed at the end of the resort. There are 5 Villas. Villa has amazing valley and mountain view ground floor






LANDSCAPE



 

WORKING DRAWING

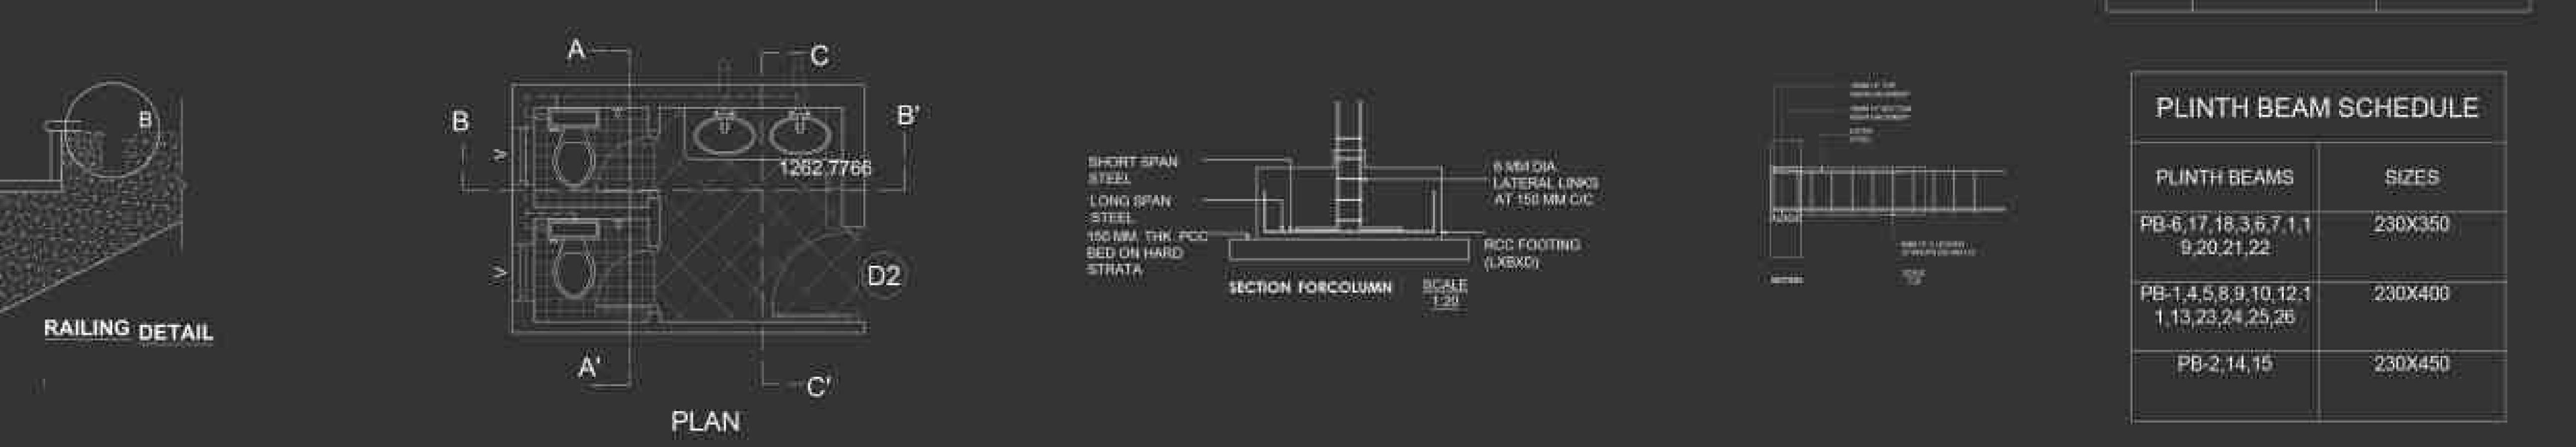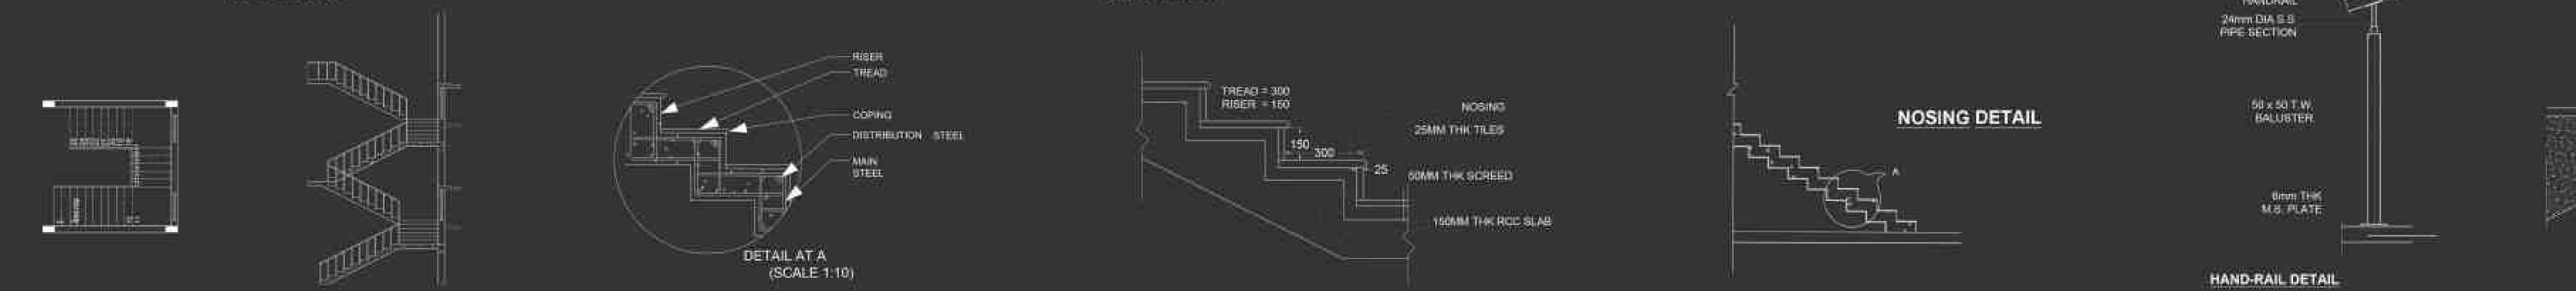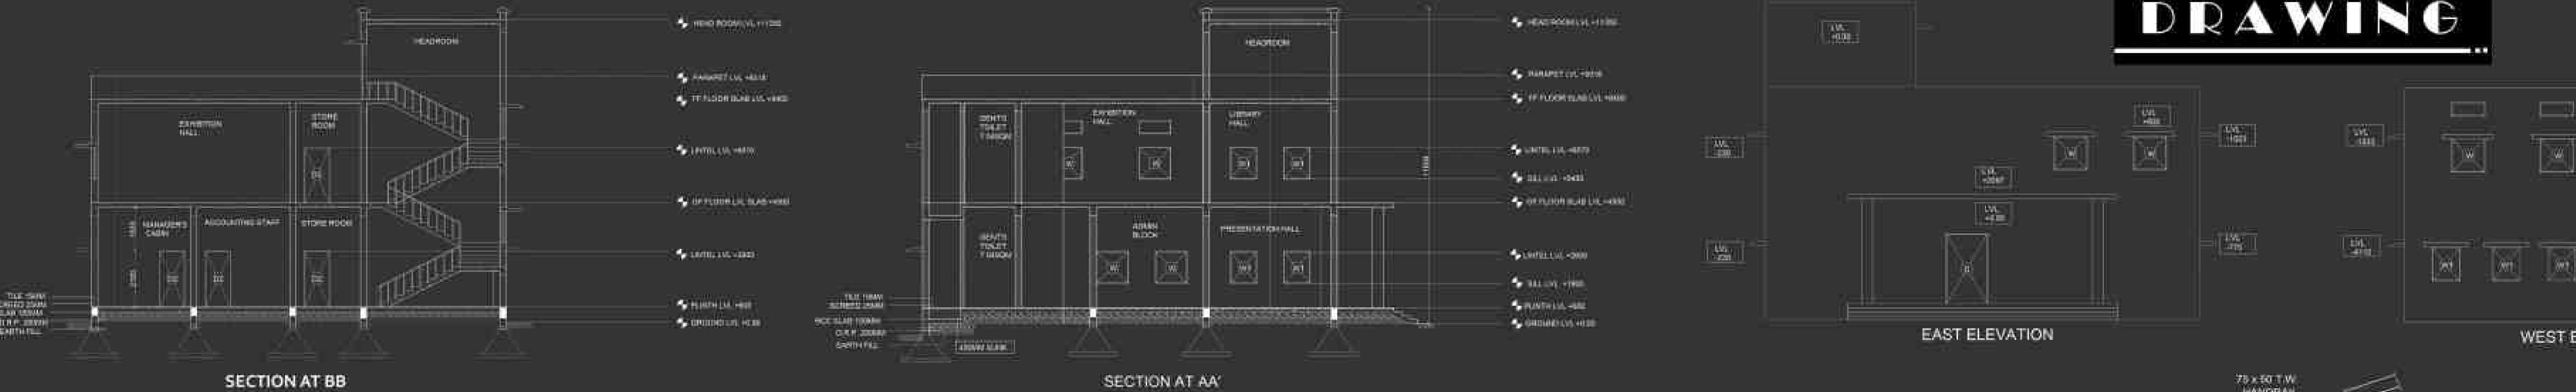

THANK YOU